

Parque costero del río Xanaes · vegetación nativa, equipamiento, circulaciones y sistema de agua



VEGETACIÓN (bloques)

- Algarrobo blanco (20 u.)
- Chañar (24 u.)
- Tala (70 u.)
- Espinillo (33 u.)
- Sauce criollo (78 u.)
- Celbo (52 u.)
- Arbustos nativos (chilca, sen) (51 u.)

EQUIPAMIENTO (bloques)

- Luminaria LED h 4.5 m (20 u.)
- Banco de hormigón y madera (16 u.)
- Mesa de picnic (4 u.)
- Reposera fija sobre deck (12 u.)
- Posta saludable (9 u.)
- Juego infantil (3 u.)
- Biciclettero (5 u.)
- Cantero elevado de huerta (27 u.)

- Paseo costero 4 m (hormigón permeable)
- Sendero de ribera 2,2 m (granular)
- Ciclovia 2,6 m
- Jardín de lluvia / cuneta verde
- Paseo-agua
- Humedal
- Inundación Q100 +332.80
- Gaviones (bordes de terrazas)

CUADRO DE EQUIPAMIENTO Y ARBOLADO (conteo de bloques en planta)

| Bloque       | Cant. | Bloque                 | Cant. |
|--------------|-------|------------------------|-------|
| Arbusto      | 51    | Cantero                | 27    |
| Algarrobo    | 20    | Deck Reposera          | 12    |
| Celbo        | 52    | Juego                  | 3     |
| Chañar       | 24    | Luminaria              | 20    |
| Espinillo    | 33    | Mesa Picnic            | 4     |
| Sauce        | 78    | Posta                  | 9     |
| Tala         | 70    | Árboles nuevos (total) | 328   |
| Banco        | 16    |                        |       |
| Biciclettero | 5     |                        |       |

CRITERIOS DE PROYECTO

- Circulaciones jerarquizadas: ciclovia y vereda arbolada sobre la Av. Costanera; paseo costero continuo en T1, a salvo de las crecidas, que une las cinco agujas; sendero de ribera en T2 para el contacto con el agua.
- Cruces peatonales elevados frente a cada aguja: la avenida se vuelve permeable y el parque se integra a la trama de Pilar.
- Arbolado según la frecuencia de inundación: algarrobo y chañar en T1, espinillo y tala en T2, sauce y celbo en T3.
- Iluminación LED cada 26 m sobre el paseo, sin iluminar la ribera para no afectar la fauna.
- Mobiliario resistente al agua: hormigón, madera dura y acero galvanizado.

PROGRAMA POR SECTOR

- RELAJACIÓN: decks con reposeras, mesas de picnic, pradera de descanso.
- DEPORTIVO: canchas de césped natural inundables, vestuarios en T1, bicicletteros.
- COMERCIAL: plaza de arbo con fena, SUM y gradas al río (ver plano de detalle).
- RECREACIÓN FÍSICA: postas saludables a lo largo del paseo, juegos infantiles.
- HUERTA: canteros elevados, vivero de nativos, compost y cisternas de agua de lluvia.

SUPUESTOS


Los bloques y cantidades surgen de la ubicación en planta de esta etapa. Los niveles de crecida son estimados a partir de las curvas de nivel del relevamiento y deben verificarse con datos hidrológicos oficiales.

CORTES-VISTA A-A Y B-B


ESC. 1:250

Secciones con vistas en elevación: ciudad, avenida, terrazas, pasarelas, vegetación nativa y crecidas

CORTE-VISTA A-A · SECTOR 1 RELAJACIÓN — ESC. 1:250

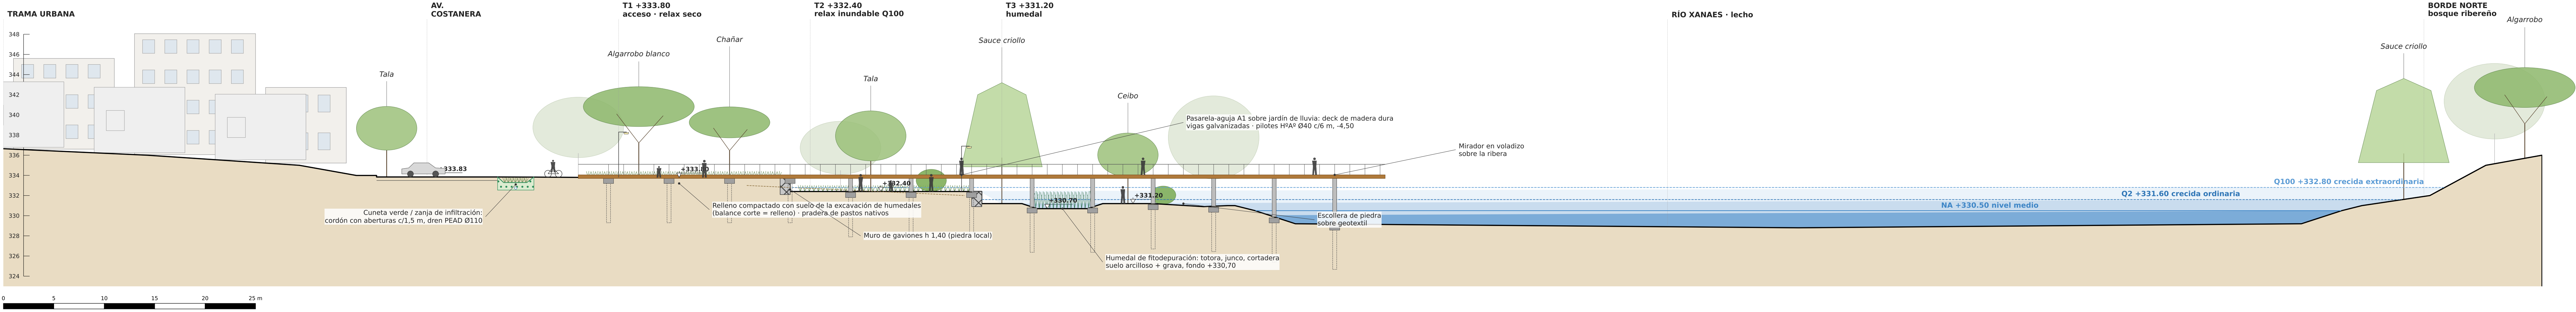

CORTE-VISTA B-B · SECTOR 2 DEPORTIVO — ESC. 1:250

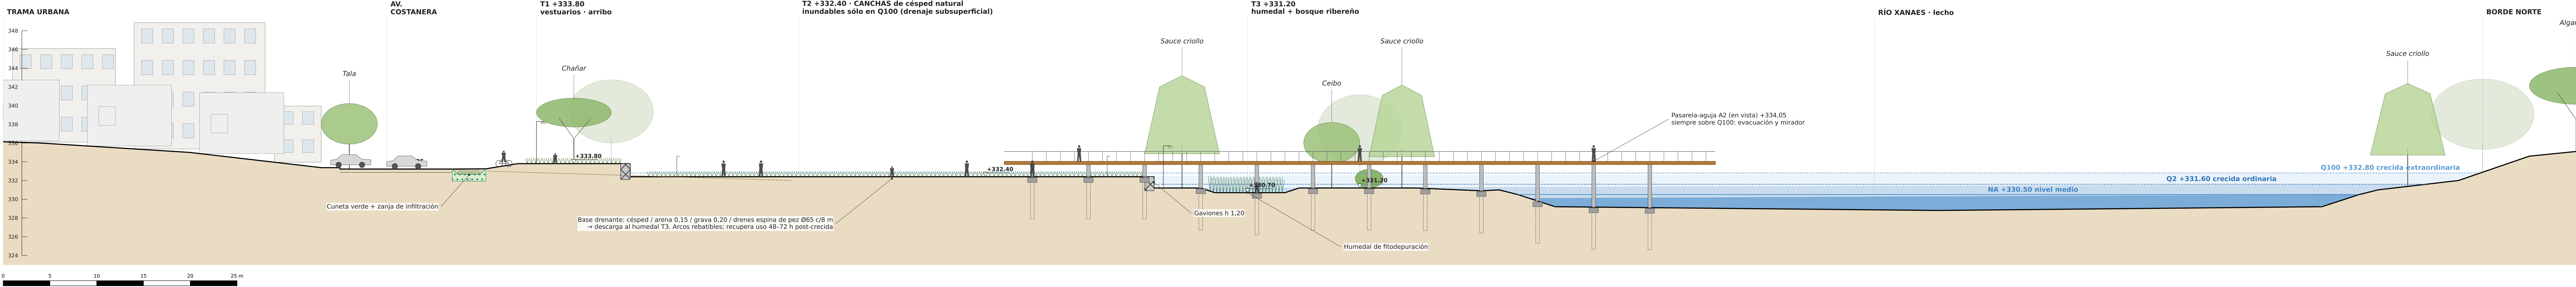


LECTURA DE LOS CORTES-VISTA

- En primer plano (línea gruesa) la sección del terreno proyectado, estructuras y vegetación cortada; en segundo plano (gris claro) las copas del arbolado y los edificios en elevación.
- De izquierda a derecha: trama urbana de Pilar (2 a 4 niveles) → vereda arbolada y Av. Costanera con cuneta verde y ciclovía → T1 seca con paseo costero y luminarias → gaviones → T2 inundable (relajación / canchas) → gaviones → T3 humedal y bosque ribereño → río Xanaes y margen norte.
- La pasarela-aguja se mantiene horizontal a +334.05, siempre por sobre la crecida Q100; es mirador, recorrido y vía de evacuación.
- Las figuras humanas (h 1.72 m) dan la escala: el desnivel total ciudad-río es de unos 7 m.

- Terreno proyectado (en corte)
- Terreno natural existente
- Vegetación en vista (fondo)
- Edificios en elevación
- Pasarela / pilotes HPAF
- Gaviones
- Q100 +332.80
- Q2 +331.60
- NA +330.50

Plaza de arribo en corte-vista - sectores 1 y 2 en planta de detalle

CORTE-VISTA C-C • SECTOR 3 PLAZA DE ARRIBO — ESC. 1:250

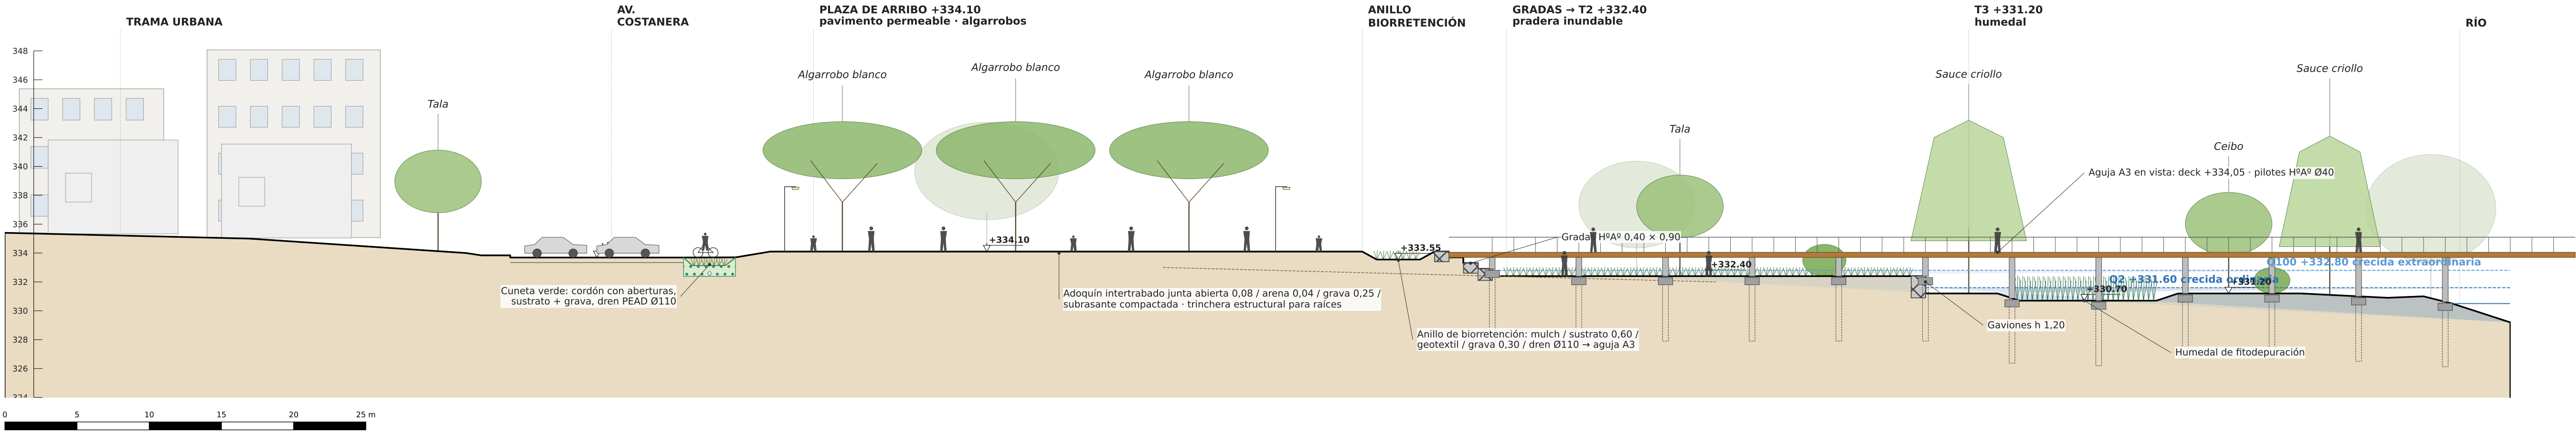

PLANTA AMPLIADA — NOTAS

- Cada aguja arranca con un cruce peatonal sobre la Av. Costanera y un ciccletero; la cuneta verde recibe el agua de la calle y la entrega al jardín de lluvia bajo la pasarela.
- El paseo costero (4 m, hormigón permeable) corre en T1 y está siempre fuera de la mancha Q100; el sendero de ribera (2.2 m, granular compactado) recorre T2.
- Sector 1: tres decks de madera con reposeras fijas orientadas al río, mesas de picnic bajo algarrobos, pradera de descanso inundable.
- Sector 2: canchas de césped natural en T2 con base drenante; vestuarios en T1 junto a la avenida; tribuna natural en el talud.
- Bosque ribereño de sauce criollo y ceibo en T3, con arbustos nativos; se conserva la vegetación existente.
- Cotas en m s.n.m.; curvas de nivel del relevamiento cada 1 m.

PLANTA AMPLIADA SECTORES 1 RELAJACIÓN Y 2 DEPORTIVO — ESC. 1:500

