

BARRIO PARQUE LINEAL

Borde noreste de Pilar - Proyecto Urbano Residencial

MEMORIA DESCRIPTIVA

ENCAJE DEL ÁREA PROYECTO EN LA E.U. DE PILAR. El ámbito (26,06 ha) es un vacío urbano en el borde noreste de Pilar, entre la cuadrícula consolidada de la ciudad y el corredor del río Segundo, al sur del área B.

- PROBLEMAS
- Discontinuidad de la trama y borde urbano sin definir hacia el río.
 - Déficit de espacios verdes cualificados y de equipamientos en el sector.
 - Crecimiento disperso de baja densidad y calles sin consolidar.
 - Riesgo de ocupación informal de un suelo vacante de gran tamaño.

- OPORTUNIDADES
- Suelo vacante sin parcelar ni preexistencias edilicias.
 - Continuidad directa con la cuadrícula y sus redes de infraestructura.
 - Cercanía a la RP N°13 y a la autopista Córdoba-Rosario.
 - Paisaje del río Segundo y del monte nativo linderó; pendiente suave (≈0,5 %) hacia el río.




PROPUESTA DE PROYECTO URBANO
Casos referenciales: el ecobarrio Vauban (Friburgo), por la movilidad peatonal y el verde de proximidad, y el Parque Lineal del río Suquia (Córdoba), por el parque como borde y estructura.

Estructura urbana: se prolonga la cuadrícula de Pilar con 13 manzanas y calles de 15 m (veredas de 2,5 m y calzada de 10 m) que completan la red existente. Un parque lineal de 2,63 ha define el nuevo borde hacia el río y articula el sistema de espacios verdes con tres plazas en el frente oeste.


Tejido urbano: tres tejidos graduados. R1: vivienda agrupada de 2 pisos. R2: vivienda colectiva de 3 pisos. R3: edificios de 4 pisos con comercio en planta baja frente al parque. La altura crece hacia el parque y conforma un frente urbano con centralidad barrial.

Paisaje urbano: arbolado de alineación en todas las veredas, patios verdes privados (F.O.S. medio 0,35) y un equipamiento público de 2,05 ha como plaza cívica y nodo de servicios.

Indicadores resultantes: 263 viviendas - 789 hab. - 10,1 viv./ha bruta - F.O.T. 1,00 - 16,4 % E.V. - 7,9 % equipamiento - 22,9 % viario - 52,8 % suelo residencial - 54,1 m² de E.V. por habitante.

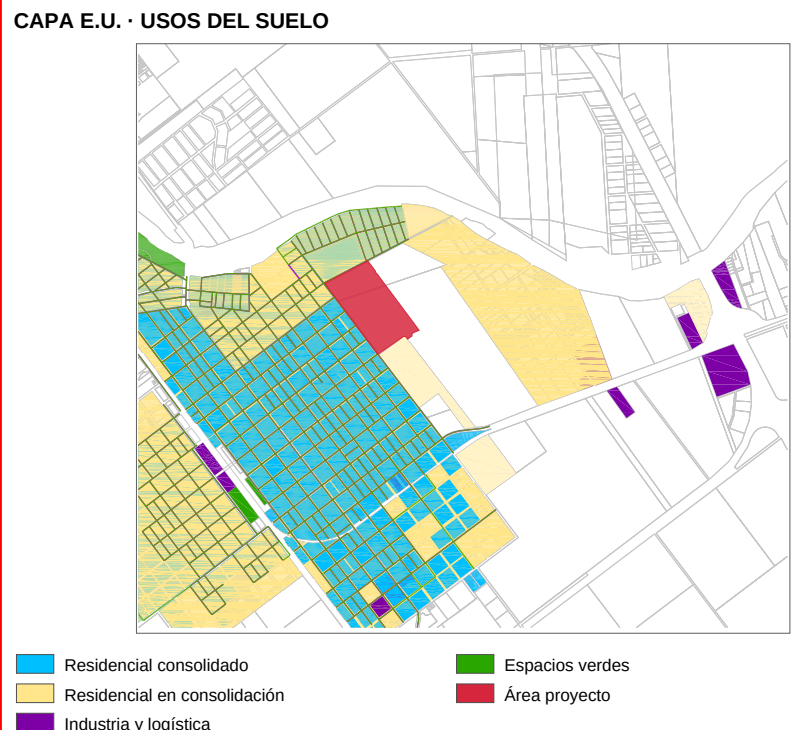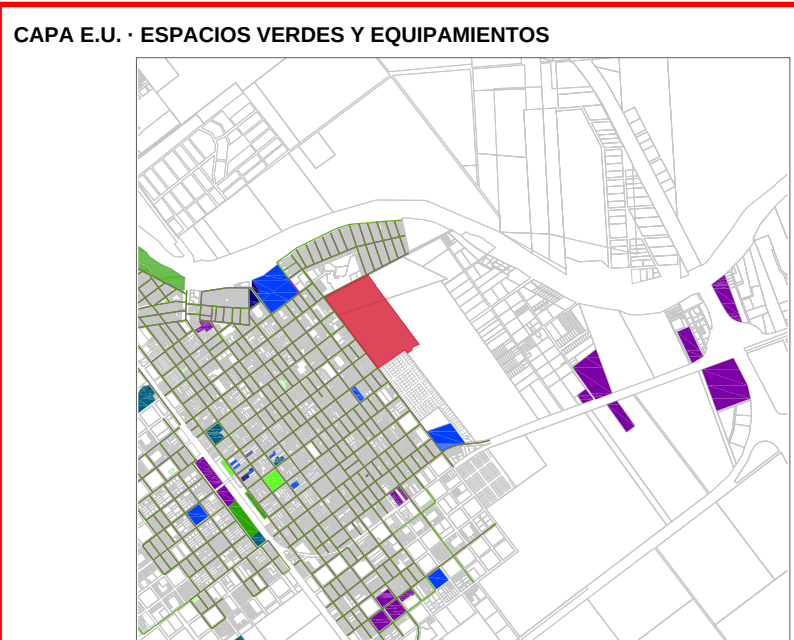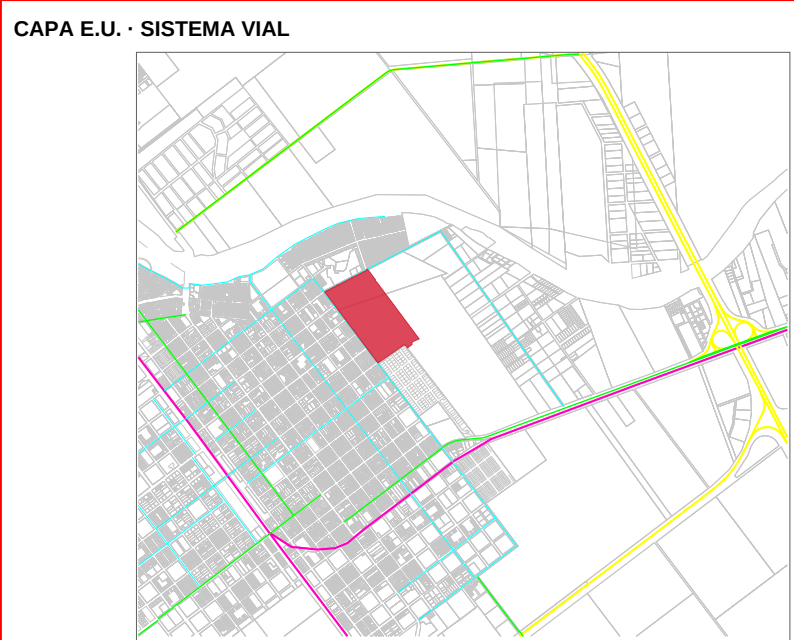

Capas elaboradas sobre la base cartográfica de la cartografía digital del INIA.

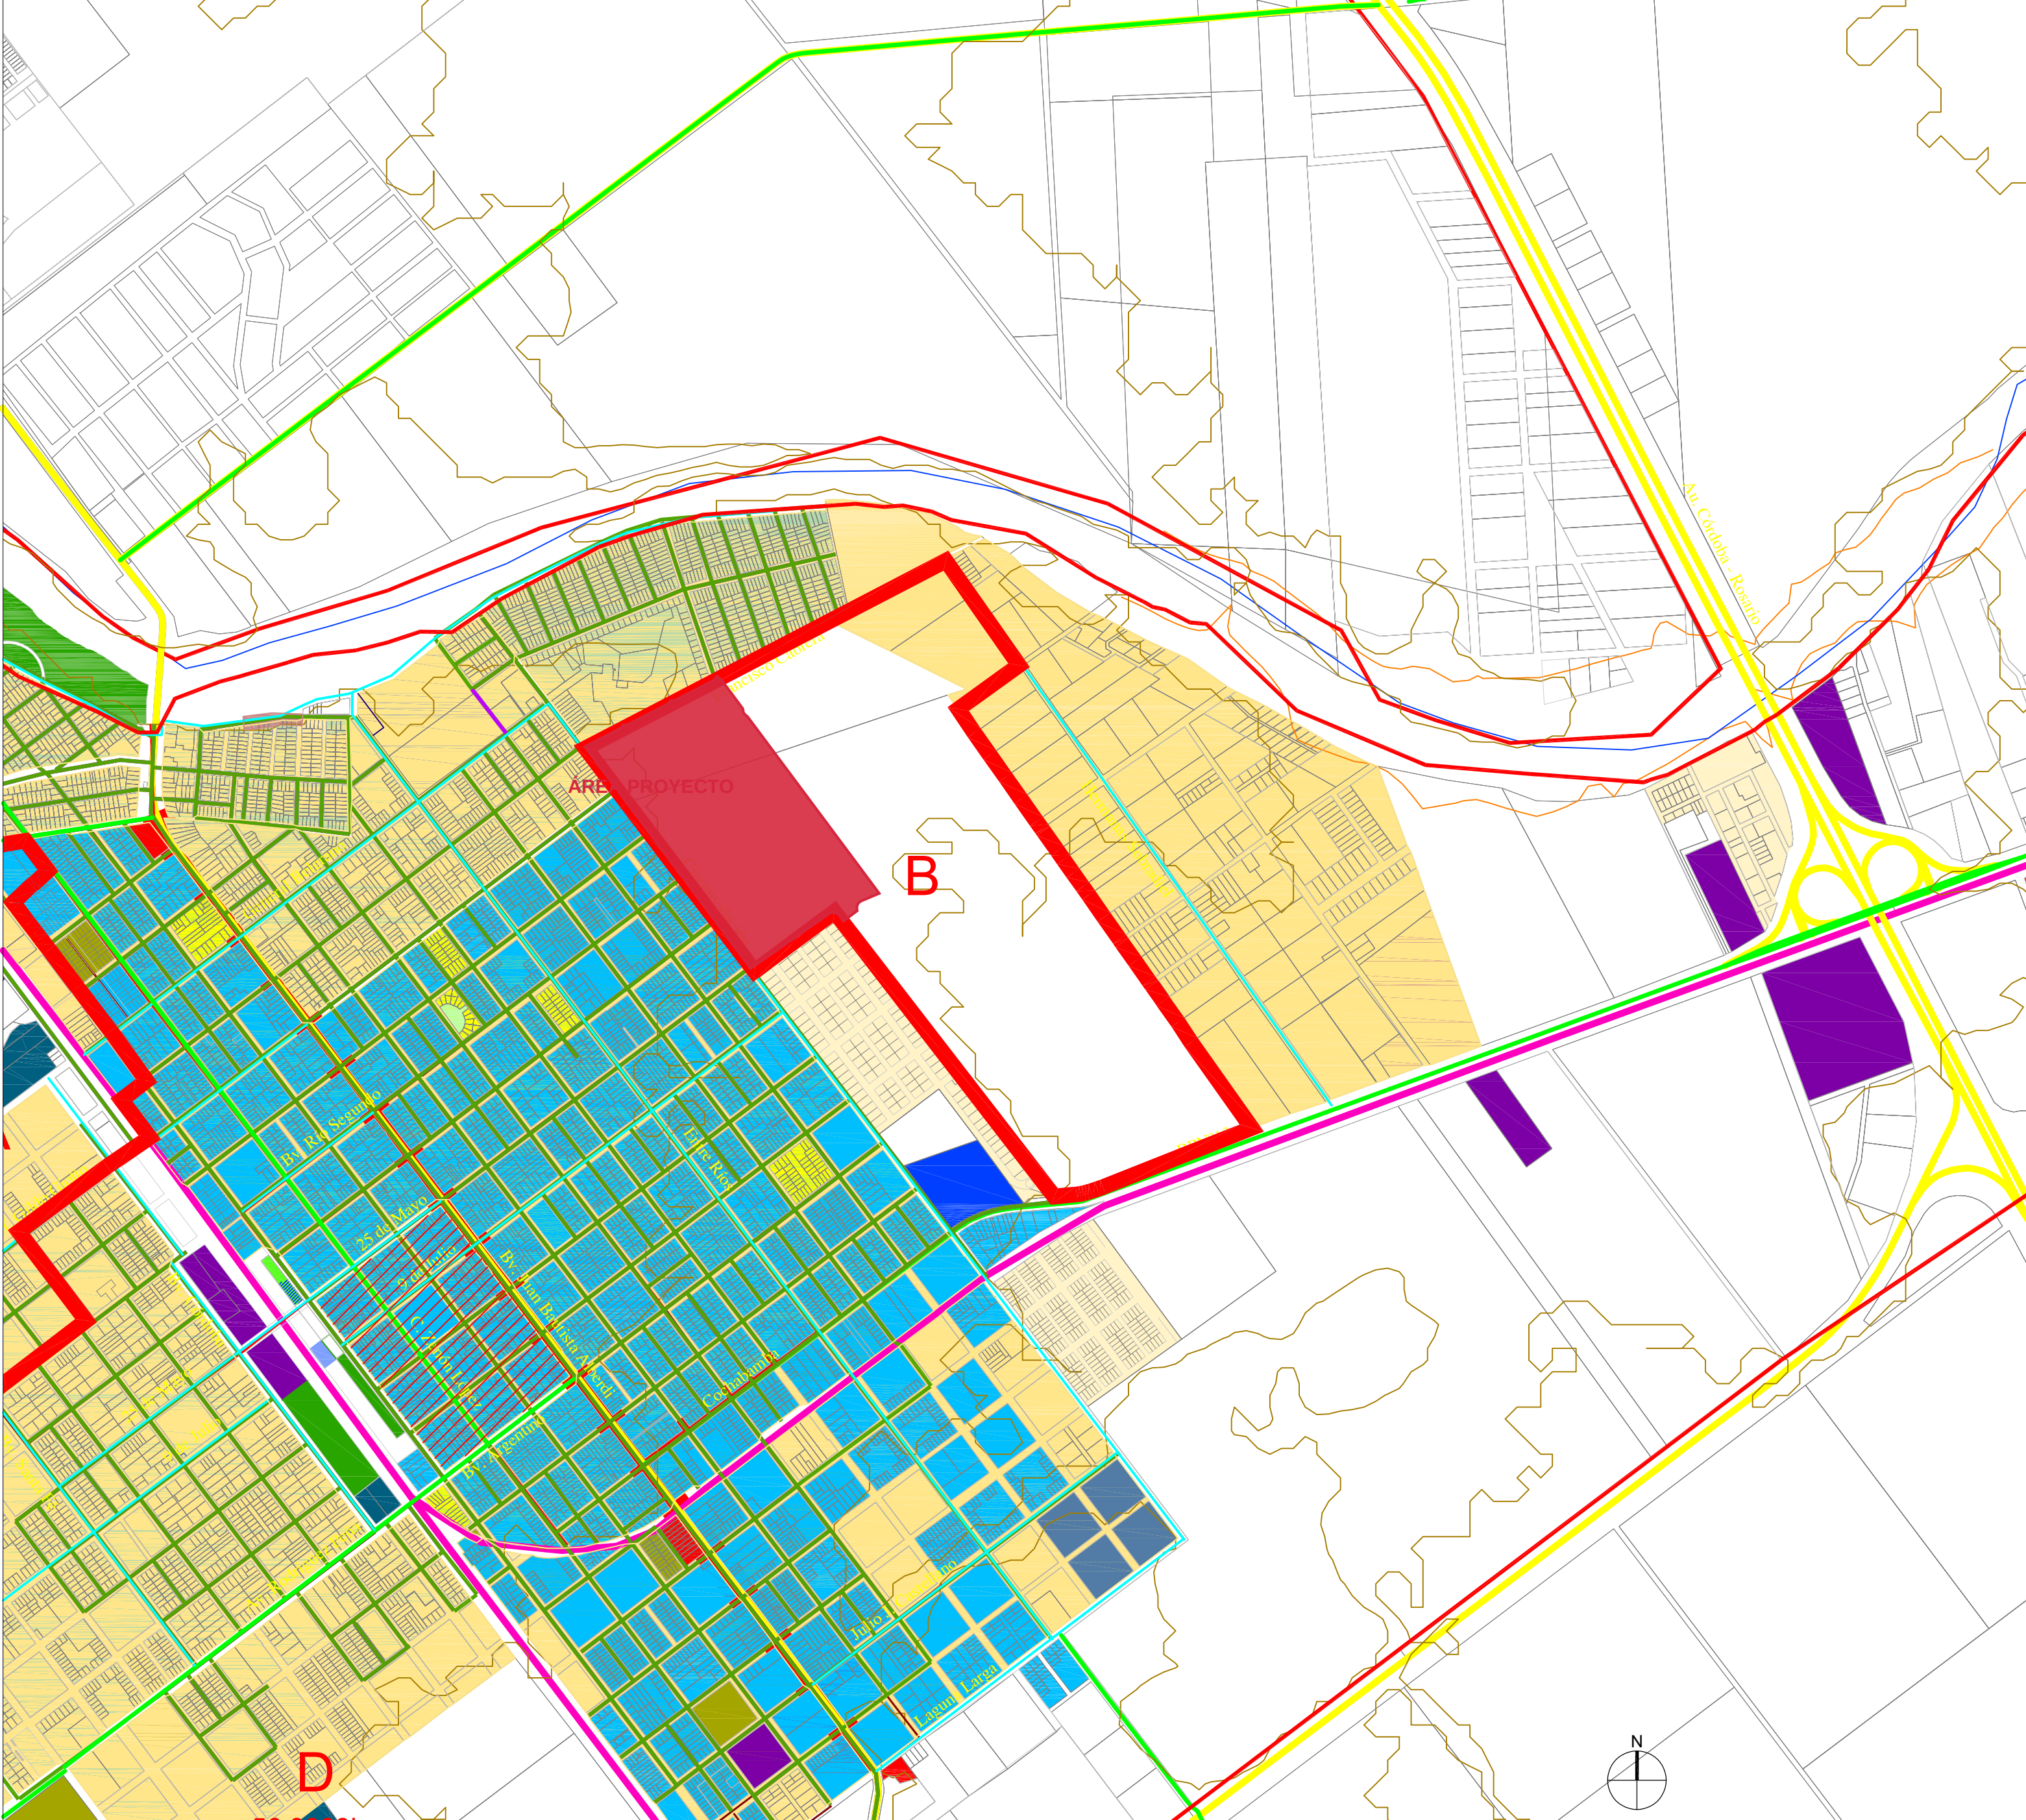

ENCAJE DE LA PROPUESTA EN LA ESTRUCTURA URBANA ESC. 1/12.500

- REFERENCIAS
- Edificación (cuerpo) y sombras
 - Espacio verde público
 - Sendas / solados
 - Pisos y jardines privados
 - Calzadas
 - Veredas alineadas
 - Área de implantación del equipamiento
 - Arbolado



PLANIMETRÍA DE LA PROPUESTA DE ORDENACIÓN URBANA DEL ÁREA PROYECTO ESC. 1/1.250






AXONOMÉTRICA DEL CONJUNTO DE LA PROPUESTA DE ORDENACIÓN URBANA DEL ÁREA CON IMÁGENES DE RECORRIDO



1 - Frente comercial sobre el parque lineal 2 - Calle local arbolada (vista hacia el parque)

INDICADORES DE SOSTENIBILIDAD - ENFOQUE SOCIO-AMBIENTAL

MODELO DE GESTION PROPUESTO

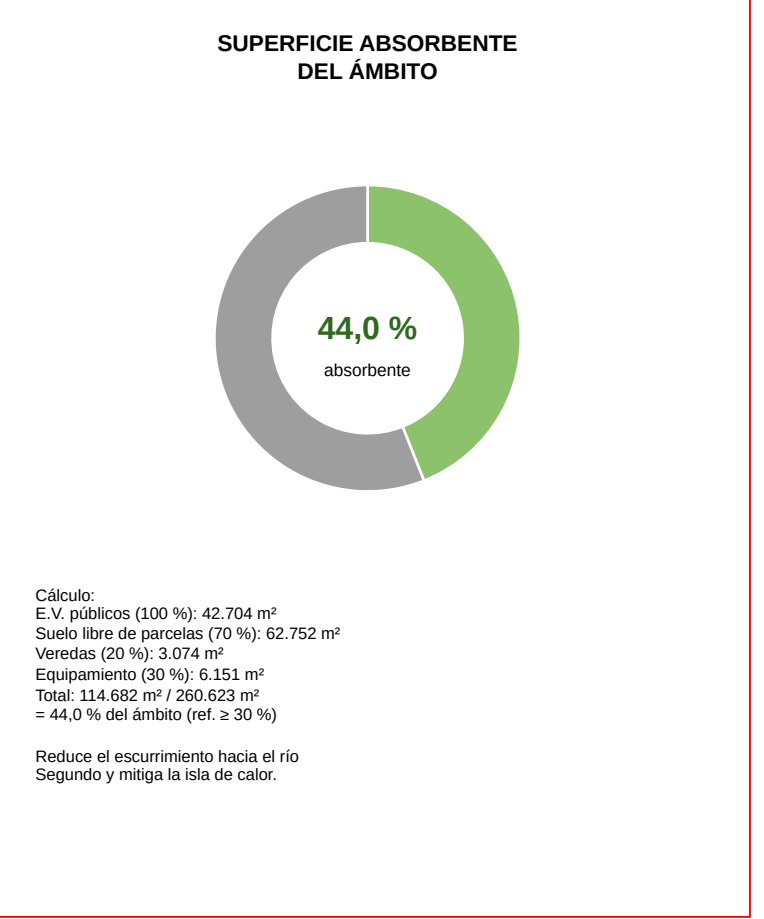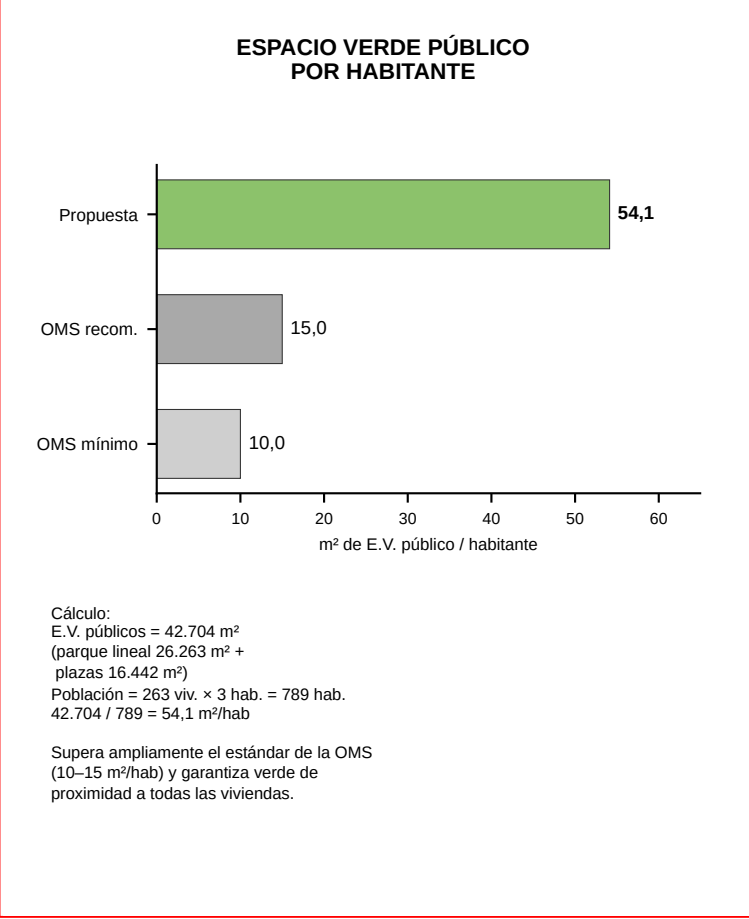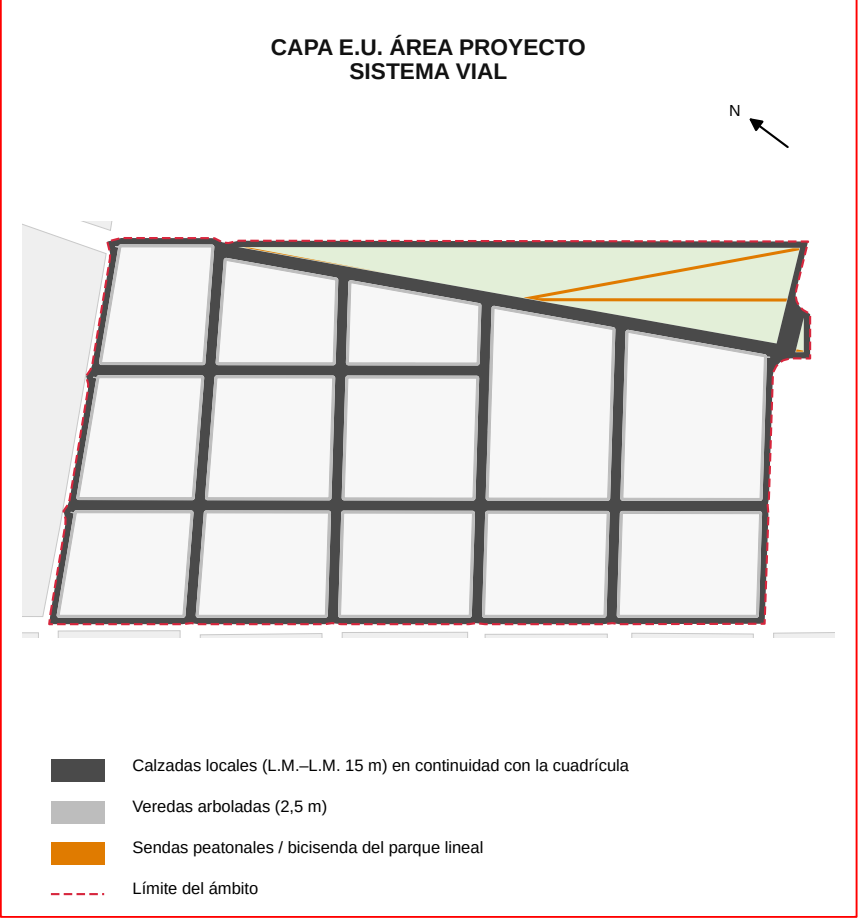

MODELO DE GESTIÓN
Contexto: urbanístico (ámbito privado (Municipalidad de Pilar y propietarios del suelo) mediante una unidad de actuación única con equipamiento de barrio).

- Cesiones gratuitas al municipio: viario, espacios verdes y equipamiento (>47 % del ámbito).
- Recuperación de plusvalías por el caso de suelo rural a urbano, en suelo o en obras de infraestructura (agua, cloaca, pavimento, alumbrado).
- Ejecución por etapas: E1 manzanas contiguas al tejido existente (zonas de red); E2 parque lineal y frente comercial; E3 equipamiento público.
- Caso de vivienda social en la tipología R1 a través de programas provinciales y nacionales.
- Mantenimiento del parque lineal por un consorcio vecinal junto con el municipio.

789	POBLACIÓN (hab.)	263	VIVIENDAS (viv.)	30,3	DENSIDAD POBLACIONAL (hab./ha.)	10,1	DENSIDAD BRUTA (viv./ha.bruta)	19,1	DENSIDAD NETA (viv./ha.neta)	26,06	SUP. AMBITO (ha.)	5,97 22,9%	SUP. VIARIO (ha.-%)	4,27 16,4%	SUP. ESP. VERDES (ha. - %)	2,05 7,9%	SUP. EQUIP. PUB. (ha. - %)	13,77 52,8%	SUP. PARCELAS RESIDENCIALES (ha. - %)
-----	------------------	-----	------------------	------	---------------------------------	------	--------------------------------	------	------------------------------	-------	-------------------	---------------	---------------------	---------------	----------------------------	--------------	-----------------------------	----------------	--

INDICADORES URBANÍSTICOS - ENFOQUE FÍSICO-FUNCIONAL

BARRIO PARQUE LINEAL

Borde noreste de Pilar · Proyecto Urbano Residencial

CASO DE ESTUDIO: PILAR, CÓRDOBA · CURSO 2026

ÍNDICE DE LÁMINAS

- 01 Carátula
- 02 Fotoplano
- 03 Preexistencias y estructura de la propiedad
- 04 Sistemas urbanos · suelo de uso público
- 05 Zonas · suelo de uso privado
- 06 Ordenación de la edificación
- 07 Cortes
- 08 Usos de la edificación · planta baja
- 09 Usos de la edificación · planta tipo
- 10 Planimetría de conjunto
- 11 Cálculos urbanísticos

DATOS DE LA PROPUESTA

Superficie del ámbito	26,06 ha
Viviendas	263
Población	789 hab.
Densidad bruta	10,1 viv./ha
Espacios verdes públicos	4,27 ha (16,4 %)
Equipamiento público	2,05 ha (7,9 %)
Viario	5,97 ha (22,9 %)
Suelo residencial	13,77 ha (52,8 %)





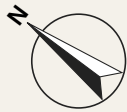


Imagen: planimetría general de la propuesta (sin escala).

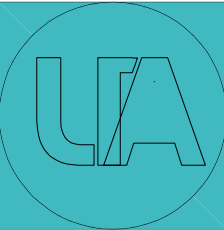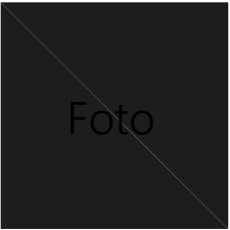

Alumno:
Alumno:
Alumno:

 

 

LEGAJO TÉCNICO · PROPUESTA DE ORDENACIÓN

LÁMINA 02

ESC. 1/1.250

FOTOPLANO

Situación actual del ámbito de intervención y su entorno inmediato.

REFERENCIAS

— · —


 Límite del ámbito de intervención

○




 Superficie del ámbito: 26,06 ha

Fuente: imagen satelital Esri World Imagery (Maxar / Earthstar Geographics), georeferenciada sobre la base catastral provista por la cátedra.

Lectura: el ámbito es un vacío urbano de borde, sin edificaciones ni parcelamiento urbano, entre el tejido consolidado de Pilar (SC) y el no Segundo (N). Lo atraviesan huellas de tránsito informal.

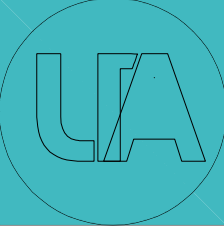



Alumno:
Alumno:
Alumno:

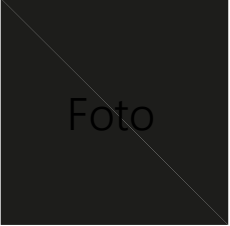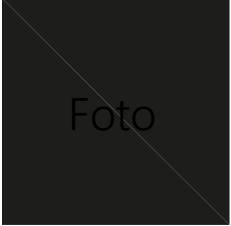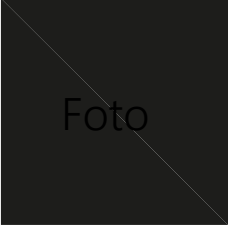

PROYECTO URBANO RESIDENCIAL

CURSO 2026
CASO DE ESTUDIO: PILAR, CBA.

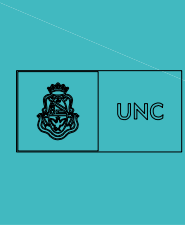

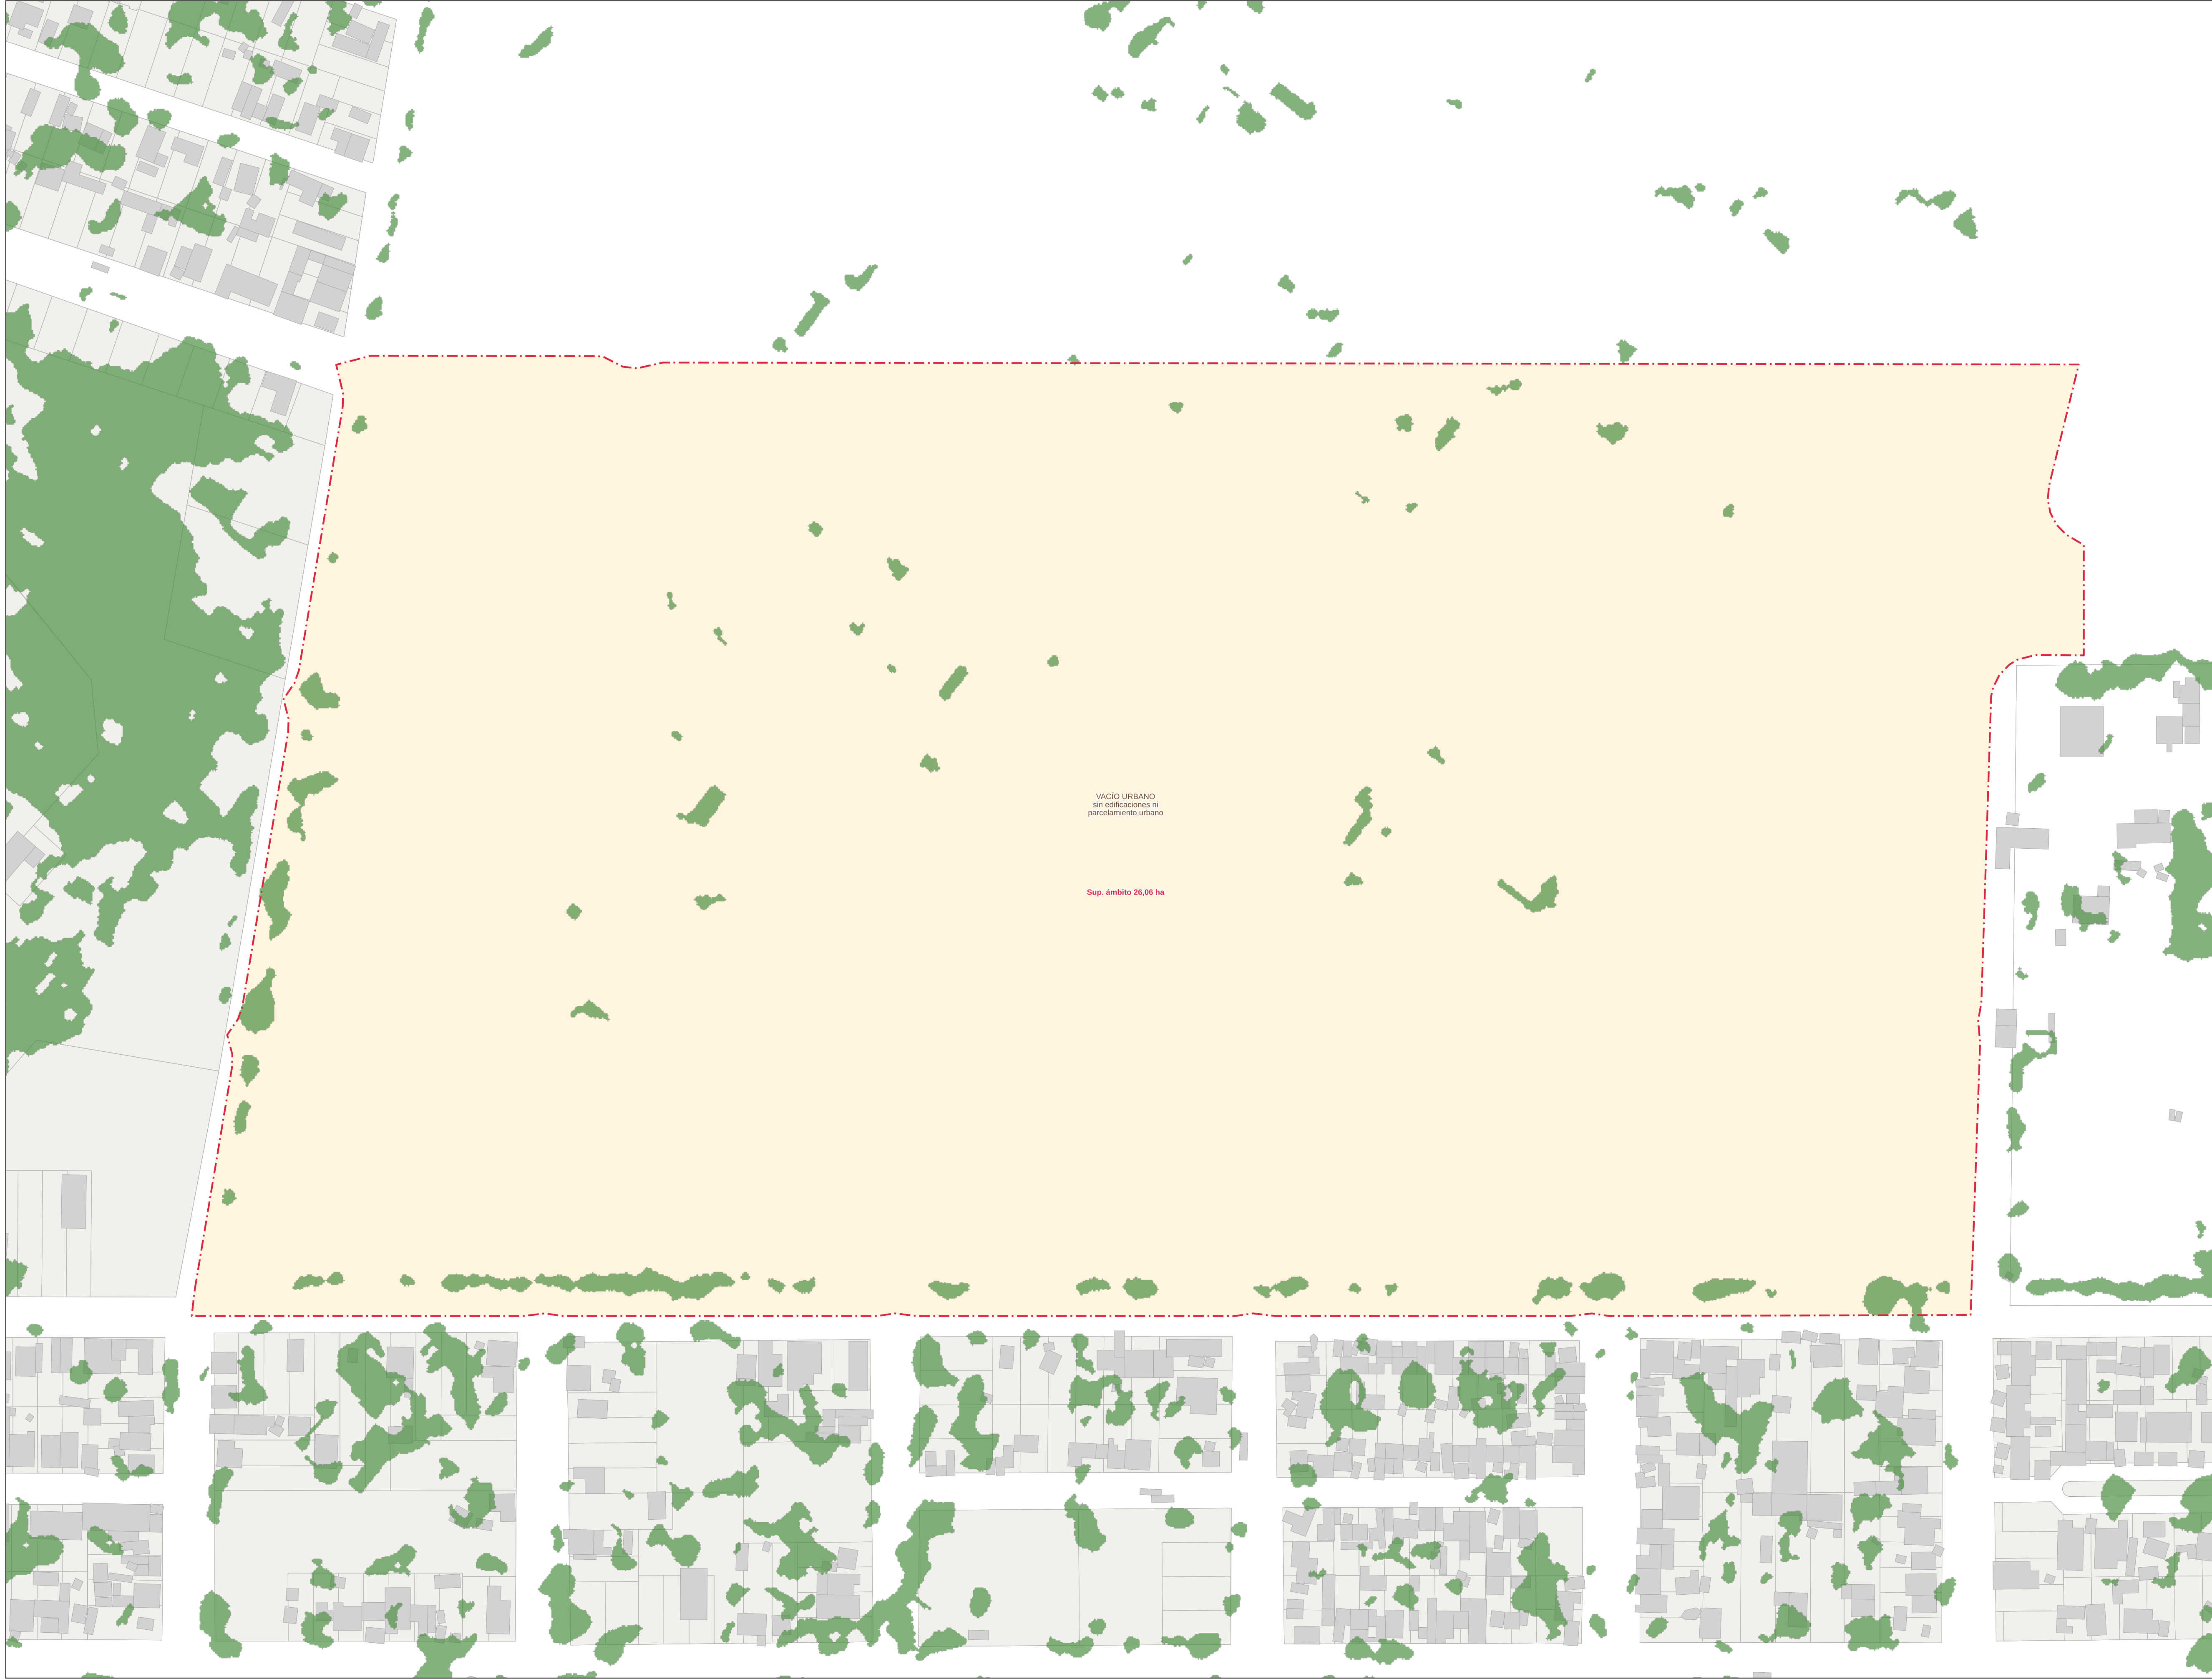

LEGAJO TÉCNICO - PROPUESTA DE ORDENACIÓN

LÁMINA 03

ESC. 1/1.250

PREEXISTENCIAS Y ESTRUCTURA DE LA PROPIEDAD

REFERENCIAS

- Límite del ámbito de intervención
- Suelo vacante (ámbito)
- Manzanas existentes (catastro)
- Parcelario existente
- Edificaciones existentes
- Arbolado / vegetación existente




ESTRUCTURA DE LA PROPIEDAD

Suelo rural indiviso, sin parcelamiento urbano ni subdivisión catastral.

Borde SO: tejido consolidado con parcelas de 10-15 m de frente y avientas de 1-2 p.

Borde NO: parcelas irregulares con monte nativo, se preserva como pulmón verde.

Si preexistencias edificas dentro del ámbito.

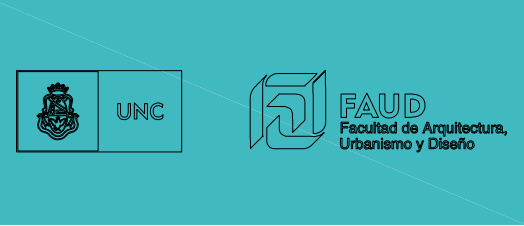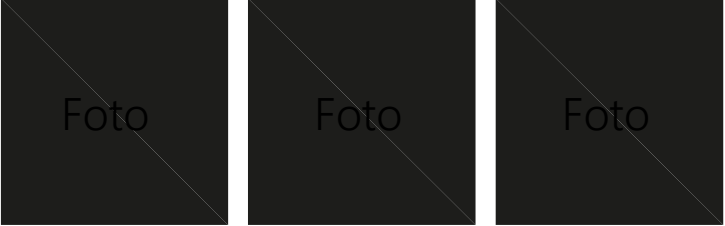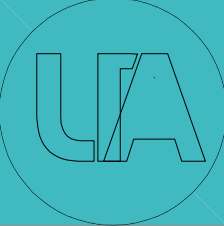



LEGAJO TÉCNICO - PROPUESTA DE ORDENACIÓN

LÁMINA 04

ESC. 1/1,250

SISTEMAS URBANOS
SUELO DE USO PÚBLICO

Red viaria, sistema de espacios verdes
y sistema de equipamientos.

012.52550100
ESC. 1/1,250

REFERENCIAS

— — —

 Límite del ámbito

SISTEMA VIARIO

Calzadas

Veredas (ancho 2.5 m)

SISTEMA DE ESPACIOS VERDES

Espacios verdes públicos

SISTEMA DE EQUIPAMIENTOS

Equipamiento público

SUELO PRIVADO

Manzanas residenciales (ver lám. 05)



SUELO PÚBLICO	m²	% ámbito
Vario (calzadas + veredas)	59.673	22,9
Calzadas	44.301	17,0
Veredas	15.372	5,9
Espacios verdes públicos	42.704	16,4
Parque lineal	26.263	10,1
Plazas en manzana	16.442	6,3
Equipamiento público	20.505	7,9
TOTAL SUELO PÚBLICO	122.882	47,1



UBICACIÓN - PILAR, CÓRDOBA

ZONAS
SUELO DE USO PRIVADO

Calificación del suelo residencial por
tipo de tejido (parcela a parcela).

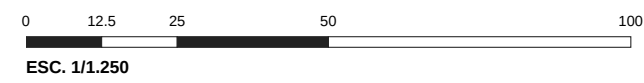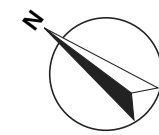

REFERENCIAS



- Límite del ámbito
- R1 - Residencial densidad baja
vivienda agrupada 2 pisos
- R2 - Residencial densidad media
vivienda colectiva 3 pisos
- R3 - Residencial mixta densidad media
4 pisos, comercio en PB
- Suelo público: espacios verdes
- Suelo público: equipamiento

ZONA	Parc.	Sup. m²	%	Viv.
R1	37	38.344	14,7	74
R2	56	88.292	33,9	168
R3	6	11.084	4,3	21
TOTAL	99	137.721	52,8	263



ORDENACIÓN DE LA EDIFICACIÓN

Parcelamiento, implantación de la edificación, alturas (pisos), cotes y líneas de corte.

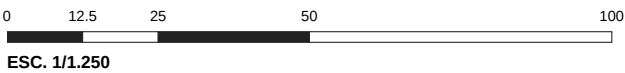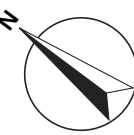

REFERENCIAS

- Límite del ámbito
- Línea municipal (L.M.) - manzana
- Línea de cordón de vereda (L.C.V.)
- Límite de parcela
- Edificación propuesta (huella)
- 3P Altura en pisos (P = pisos)
- N° de manzana / superficie m²
- 45 N° de parcela
- Línea de corte (ver lám. 07)


OCCUPACIÓN POR MANZANA

MZ	Sup. m²	Parc.	Viv.	FOS	FOT	Pisos
01	11.876	6	16	0,37	1,02	2-3
02	12.392	10	24	0,31	0,80	2-3
03	12.774	10	24	0,31	0,77	2-3
04	11.833	10	24	0,33	0,84	2-3
05	20.505	—	—	—	—	EQ
06	13.560	10	24	0,29	0,73	2-3
07	12.581	5	13	0,38	1,06	2-3
08	13.811	9	24	0,35	0,88	2-3
09	14.991	12	30	0,36	0,95	2-3
10	10.801	3	9	0,37	1,11	3
11	10.146	7	24	0,45	1,50	3-4
12	8.601	6	18	0,43	1,55	3-4
13	20.803	11	33	0,33	1,07	3-4
TOTAL	174.675	99	263	0,35	1,00	




CORTES

Cortes urbanos A-A y B-B, ampliación y perfil vial tipo.

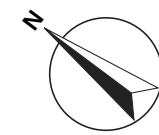


REFERENCIAS


- Vivienda agrupada 2 pisos (R1)
- Vivienda colectiva 3-4 pisos (R2/R3)
- Comercio en planta baja (R3)
- Edificio cortado
- Edificio en vista
- Terreno natural
- Arbolado
- Línea municipal (L.M.)
- Línea de cordón de vereda (L.C.V.)

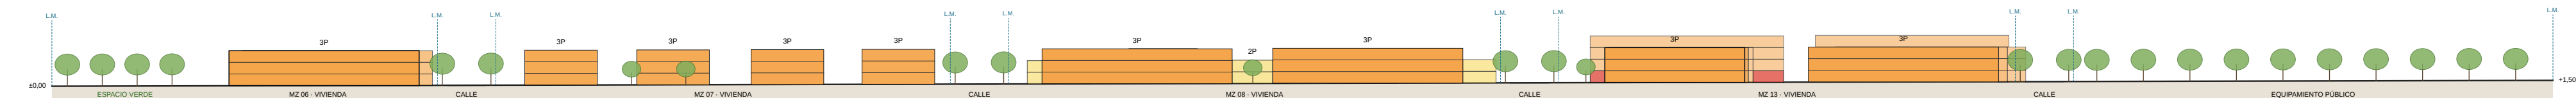


CORTE A-A · ESC. 1/1.250

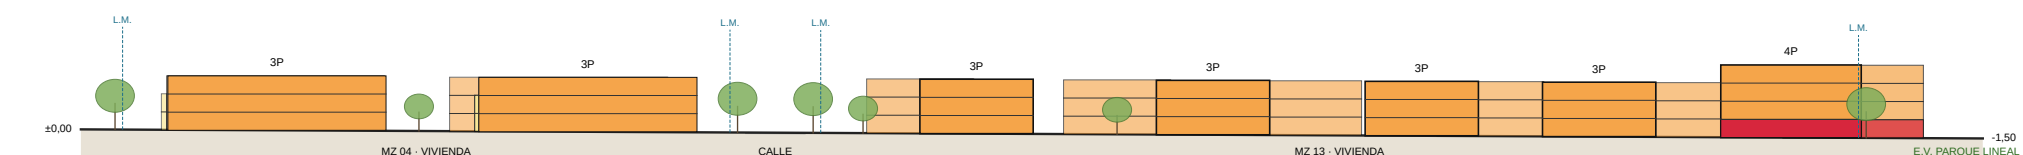


CORTE B-B · ESC. 1/1.250

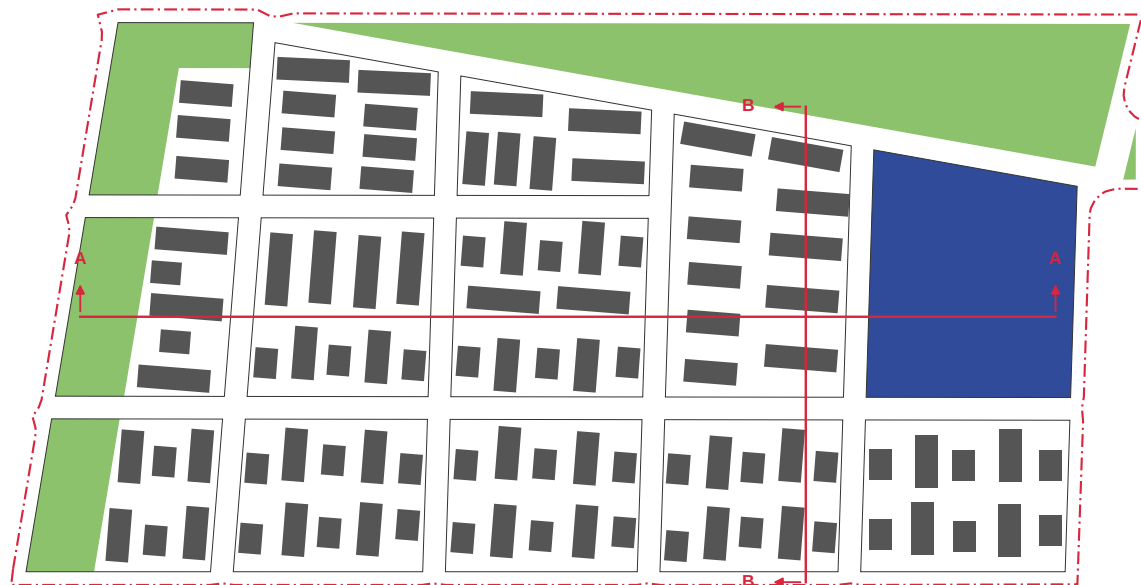


PLANTA CLAVE · ESC. 1/5.000

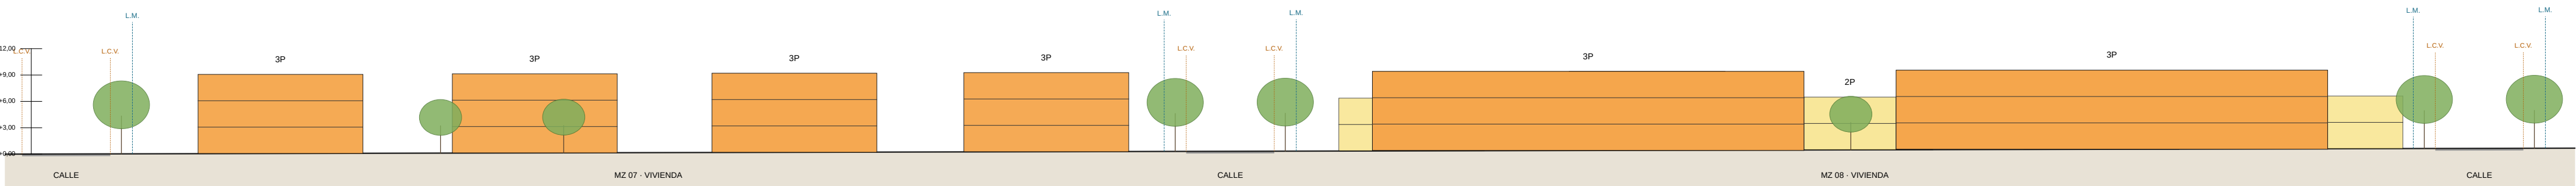

CORTE A-A · AMPLIACIÓN (MZ 07 y MZ 08) · ESC. 1/500

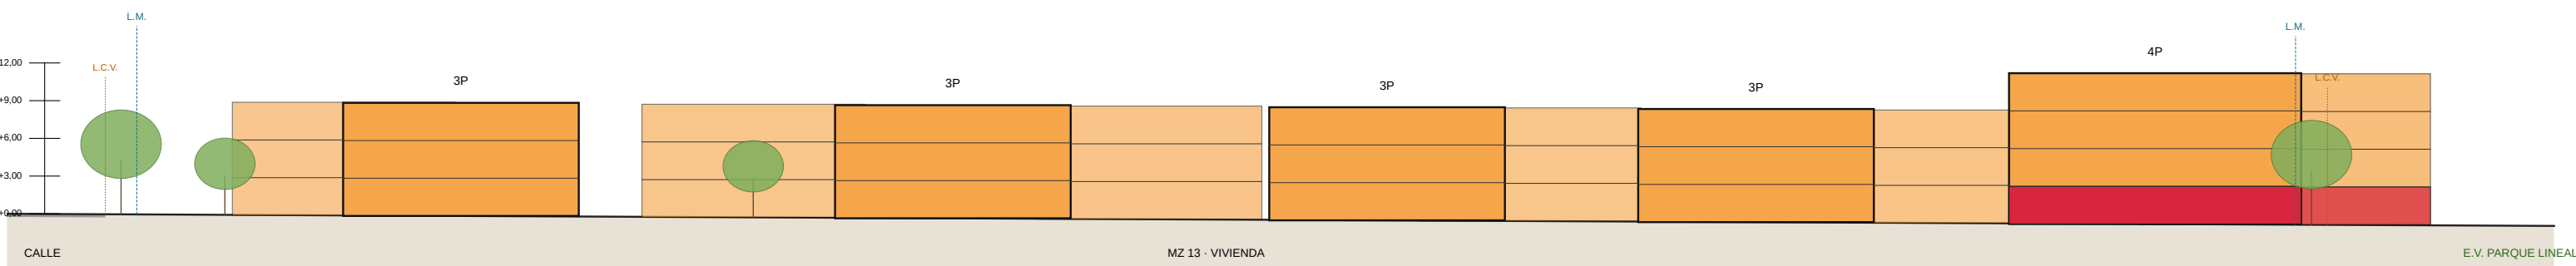

CORTE B-B · AMPLIACIÓN (MZ 13 y PARQUE LINEAL) · ESC. 1/500

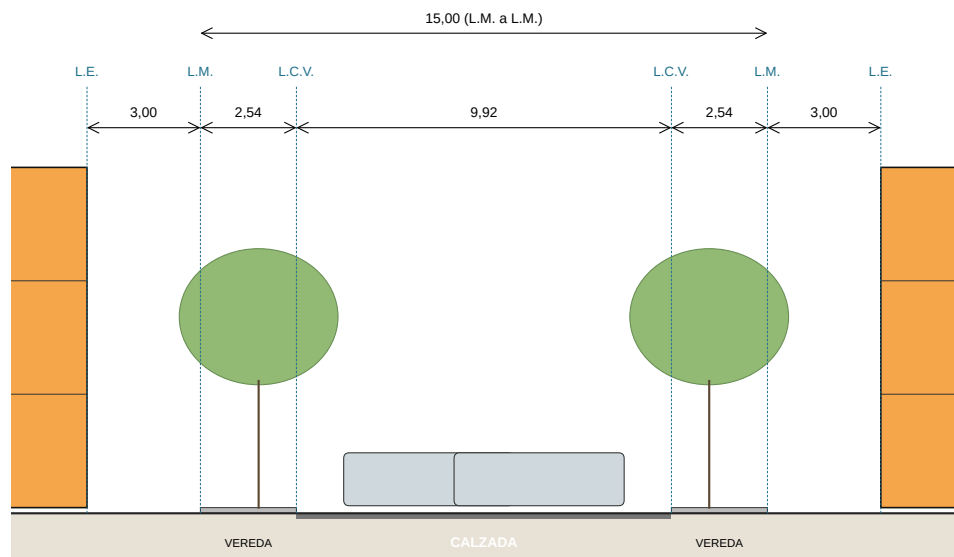



PERFIL VIAL TIPO · CALLE LOCAL · ESC. 1/200

Notas: altura de piso 3.00 m. Terreno natural con desnivel de 1.50 m en ambos cortes (pendiente general hacia el río Segundo). Los edificios cortados se representan con contorno grueso; los edificios en vista, alternados según su distancia al plano de corte. En los edificios de 4 pisos la planta baja es comercial.





USOS DE LA EDIFICACIÓN
PLANTA BAJA

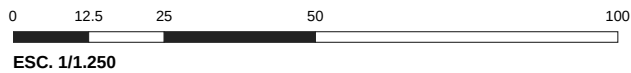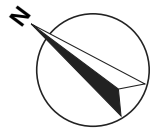

REFERENCIAS

- Vivienda
- Comercio / servicios de proximidad
- Espacio libre privado (patios / jardines)
- Espacio verde público
- Equipamiento público (a proyectar)
- Limite del ámbito

PLANTA BAJA	m²	%
Vivienda	43.035	89,5
Comercio / servicios	5.040	10,5
TOTAL CUBIERTO PB	48.075	100,0



La planta baja comercial se concentra en los edificios de 4 pisos del frente al parque lineal, conformando un eje de actividad y centralidad barrial frente al espacio verde.





USOS DE LA EDIFICACIÓN PLANTA TIPO

Pisos altos (1° a 3° piso): uso residencial exclusivo, una vivienda por planta.

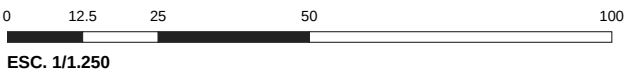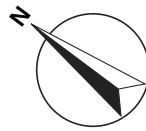

REFERENCIAS

VIVIENDA EN PISOS ALTOS

- Vivienda – edificio de 2 pisos (1 planta alta)
- Vivienda – edificio de 3 pisos (2 plantas altas)
- Vivienda – edificio de 4 pisos (3 plantas altas)

OTROS



- Espacio libre privado
- Espacio verde público
- Equipamiento público
- Límite del ámbito

PISOS ALTOS	m² cub.	Viv.
Edificios 2P	11.100	37
Edificios 3P	63.870	112
Edificios 4P	15.120	21
TOTAL PISOS ALTOS	90.090	170



PLANIMETRÍA DE CONJUNTO

Sombras, vegetación, tratamiento de superficies y patios.

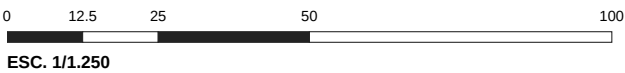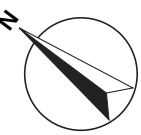

REFERENCIAS

- Edificación (cubiertas)
- Sombra proyectada (mediodía, equinoccio)
- Calzada (pavimento)
- Vereda (solado)
- Espacio verde público (césped)
- Sendas peatonales
- Solado de plaza / equipamiento
- Área de implantación del equipamiento
- Patios y jardines privados
- Galerías / expansiones privadas
- Arbolado
- Límite del ámbito

Árboles propuestos: aprox. 1019
Sombras calculadas para el sol al norte
(hemisferio sur), altura de piso 3,00 m.



A · POBLACIÓN Y VIVIENDA

INDICADOR	VALOR	UNIDAD
Viviendas	263	viv.
Habitantes por vivienda (adoptado)	3.0	hab./viv.
Población	789	hab.
Superficie del ámbito	26.06	ha
Superficie residencial neta (parcelas)	13.77	ha
Densidad bruta de viviendas	10.1	viv./ha bruta
Densidad neta de viviendas	19.1	viv./ha neta
Densidad poblacional bruta	30.3	hab./ha
Densidad poblacional neta	57.3	hab./ha neta


B · DISTRIBUCIÓN DEL SUELO (SISTEMAS Y ZONAS)

USO DEL SUELO	m²	ha	% ÁMBITO
SUELO PÚBLICO	122.882	12,29	47,1
Sistema viario	59.673	5,97	22,9
Calzadas	44.301	4,43	17,0
Veredas	15.372	1,54	5,9
Espacios verdes públicos	42.704	4,27	16,4
Equipamiento público	20.505	2,05	7,9
SUELO PRIVADO (parcelas residenciales)	137.721	13,77	52,8
R1 - Densidad baja (2 pisos)	38.344	3,83	14,7
R2 - Densidad media (3 pisos)	88.292	8,83	33,9
R3 - Mixta, comercio PB (4 pisos)	11.084	1,11	4,3
TOTAL ÁMBITO	260.623	26,06	100,0

C · OCUPACIÓN SEGÚN TIPO DE TEJIDO / TIPOLOGÍA

TIPO	Zona	Huella m²	Pisos	Cant.	Viv./edif.	Viv.	Sup. cub. m²
T1 - Vivienda agrupada	R1	300	2	37	2	74	22.200
T2 - Vivienda colectiva	R2	525	3	43	3	129	67.725
T3 - Vivienda colectiva (bloque)	R2	720	3	13	3	39	28.080
T4 - Colectiva + comercio PB	R3	720	4	7	3	21	20.160
TOTAL		48.075		100		263	138.165

G · DISTRIBUCIÓN DEL SUELO DEL ÁMBITO (% sobre 26,06 ha)

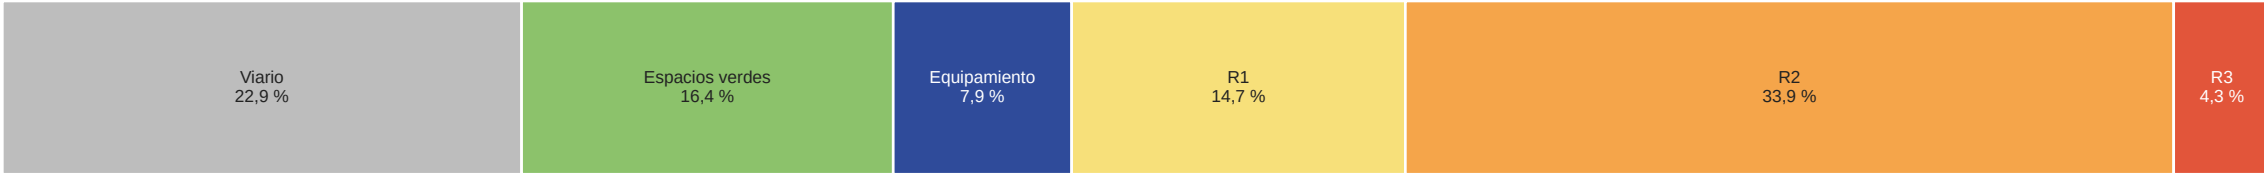

Criterios adoptados: 1 vivienda por planta; en los edificios de 4 pisos la planta baja es comercial (3 viviendas por edificio); 3 habitantes por vivienda; altura de piso 3,00 m. Superficies medidas sobre la documentación gráfica (DXF). Ámbito: manzanas, calles internas y media calzada de las calles perimetrales.

D · EDIFICABILIDAD

INDICADOR	VALOR
Superficie cubierta total	138.165 m²
Vivienda	133.125 m²
Comercio en PB	5.040 m²
F.O.S. medio (huella / sup. parcelas)	0,35
F.O.T. medio (sup. cub. / sup. parcelas)	1,00
Edificabilidad bruta (sup. cub. / ámbito)	0,53 m³/m²
Altura máxima	4 pisos - 12,00 m
Parcelas residenciales	99
Manzanas	13 (12 residenciales + 1 equipamiento)


E · INDICADORES DE SOSTENIBILIDAD

INDICADOR	VALOR	REFERENCIA
Espacio verde público por habitante	54,1 m²/hab	≥ 10–15 m²/hab (OMS)
Superficie absorbente del ámbito	44,0 %	≥ 30 %
Viviendas a < 300 m de un E.V. público	100 %	100 %
Viviendas a < 150 m de un E.V. público	61 %	—


Sup. absorbente = E.V. públicos + 70 % del suelo libre de parcelas + 20 % de veredas + 30 % del equipamiento.

F · TIPOLOGÍAS (planta y alzado esquemáticos - esc. 1/750)


T1 - Vivienda agrupada (R1)

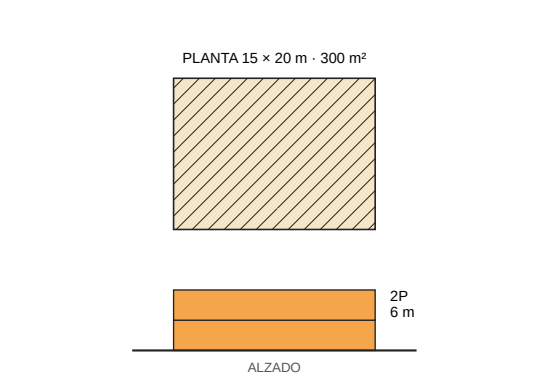


T2 - Vivienda colectiva (R2)

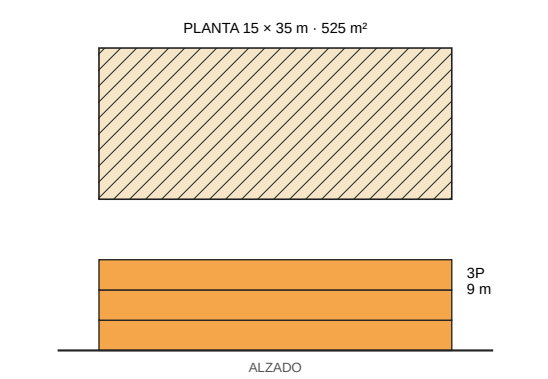

T3 - Vivienda colectiva (bloque) (R2)

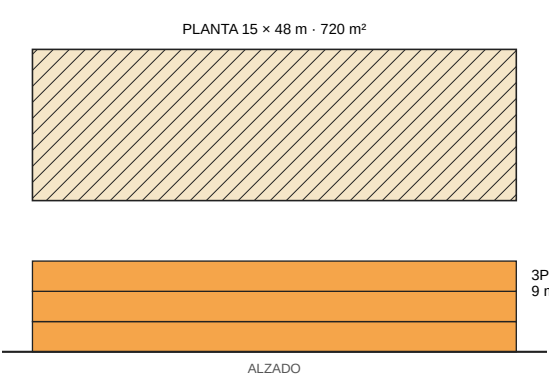

T4 - Colectiva + comercio PB (R3)

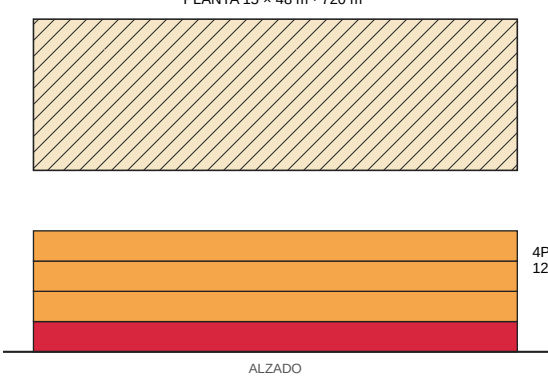

Planta baja comercial (T4)

CÁLCULOS URBANÍSTICOS

Indicadores físico-funcionales y de sostenibilidad de la propuesta.

