

BARRIO PARQUE LINEAL

Borde noreste de Pilar - Proyecto Urbano Residencial

MEMORIA DESCRIPTIVA

ENCAJE DEL ÁREA PROYECTO EN LA E.U. DE PILAR. El ámbito (26,06 ha) es un vacío urbano en el borde noreste de Pilar, entre la cuadrícula consolidada de la ciudad y el corredor del río Segundo, al sur del área B.

- PROBLEMAS
- Discontinuidad de la trama y borde urbano sin definir hacia el río.
 - Déficit de espacios verdes cualificados y de equipamientos en el sector.
 - Crecimiento disperso de baja densidad y calles sin consolidar.
 - Riesgo de ocupación informal de un suelo vacante de gran tamaño.

- OPORTUNIDADES
- Suelo vacante sin parcelar ni preexistencias edilicias.
 - Continuidad directa con la cuadrícula y sus redes de infraestructura.
 - Cercanía a la RP N°13 y a la autopista Córdoba-Rosario.
 - Paisaje del río Segundo y del monte nativo lindero; pendiente suave (≈0,5 %) hacia el río.




PROPUESTA DE PROYECTO URBANO
Casos referenciales: el ecobarrio Vauban (Friburgo), por la movilidad peatonal y el verde de proximidad, y el Parque Lineal del río Suquia (Córdoba), por el parque como borde y estructura.

Estructura urbana: se prolonga la cuadrícula de Pilar con 13 manzanas y calles de 15 m (veredas de 2,5 m y calzada de 10 m) que completan la red existente. Un parque lineal de 2,63 ha define el nuevo borde hacia el río y articula el sistema de espacios verdes con tres plazas en el frente oeste.


Tejido urbano: tres tejidos graduados. R1: vivienda agrupada de 2 pisos. R2: vivienda colectiva de 3 pisos. R3: edificios de 4 pisos con comercio en planta baja frente al parque. La altura crece hacia el parque y conforma un frente urbano con centralidad barrial.

Paisaje urbano: arbolado de alineación en todas las veredas, patios verdes privados (F.O.S. medio 0,35) y un equipamiento público de 2,05 ha como plaza cívica y nodo de servicios.

Indicadores resultantes: 263 viviendas - 789 hab. - 10,1 viv./ha bruta - F.O.T. 1,00 - 16,4 % E.V. - 7,9 % equipamiento - 22,9 % viario - 52,8 % suelo residencial - 54,1 m² de E.V. por habitante.

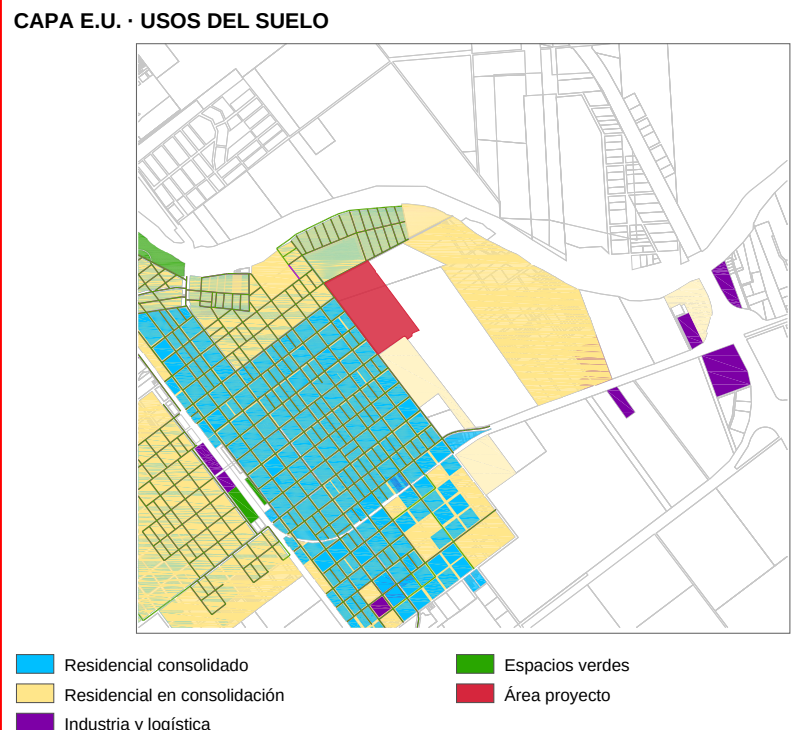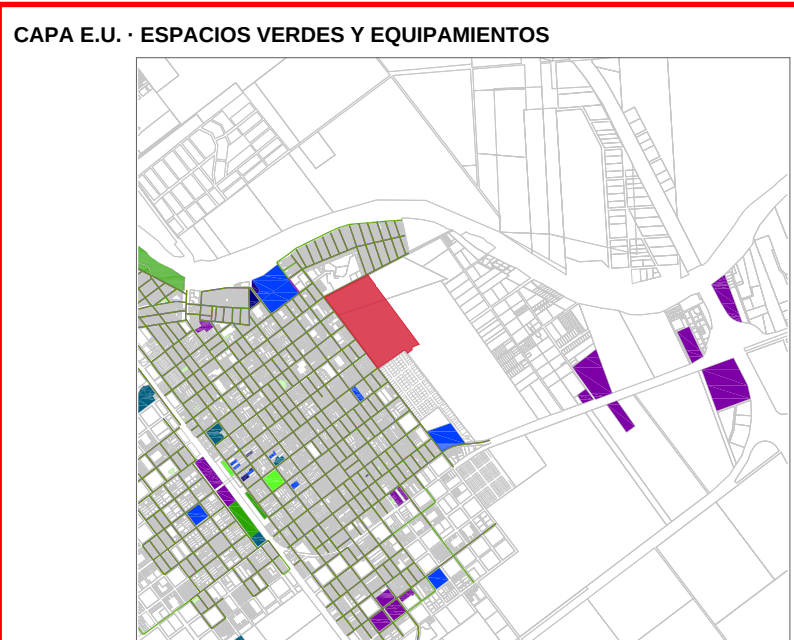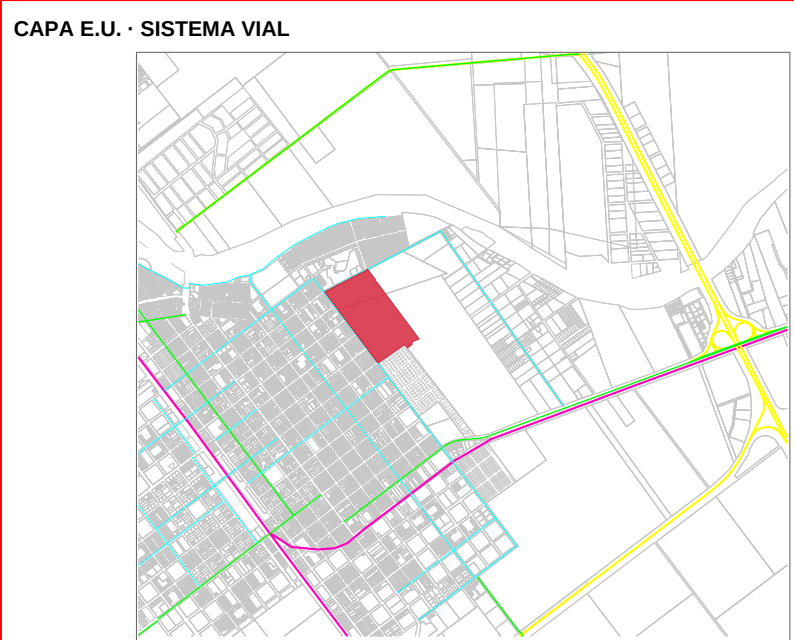

Capas elaboradas sobre la base cartográfica de la cartografía digital del INIA.

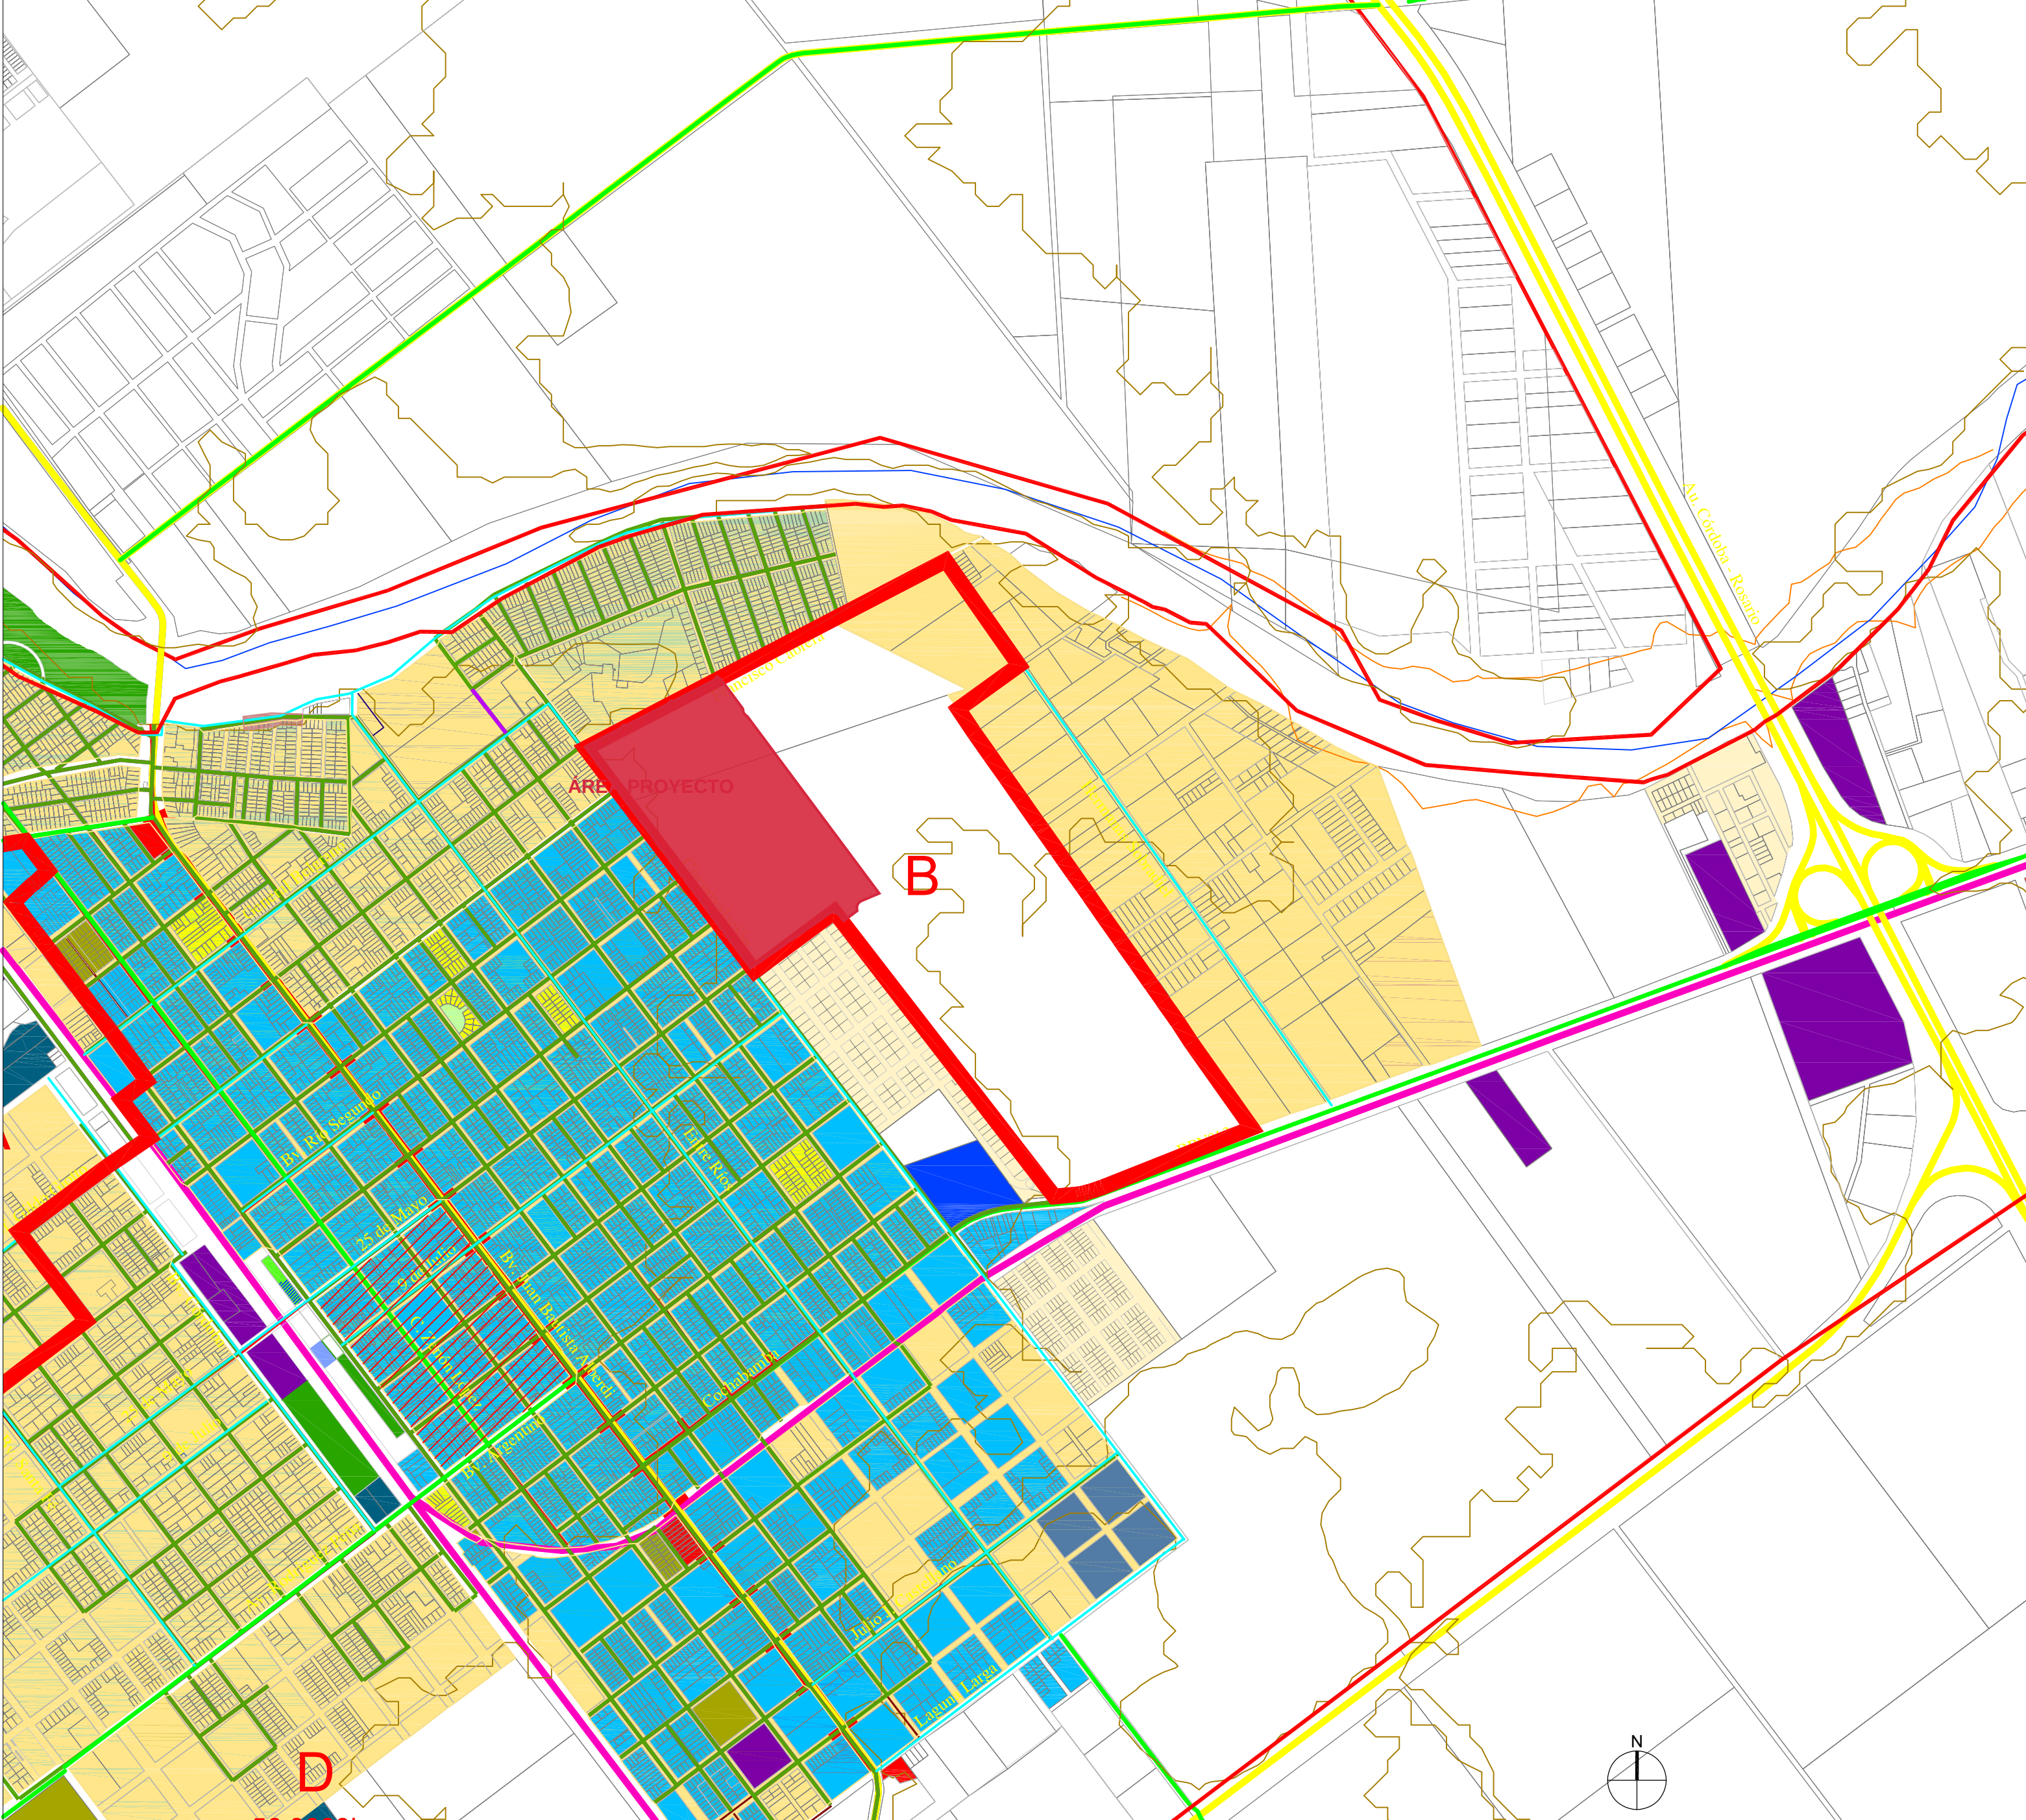

ENCAJE DE LA PROPUESTA EN LA ESTRUCTURA URBANA ESC. 1/12.500

- REFERENCIAS
- Edificación (cubiertas y sombras)
 - Espacio verde público
 - Sendas / solados
 - Pisos y jardines privados
 - Calzadas
 - Veredas alineadas
 - Área de implantación del equipamiento
 - Arbolado



PLANIMETRÍA DE LA PROPUESTA DE ORDENACIÓN URBANA DEL ÁREA PROYECTO ESC. 1/1.250






AXONOMÉTRICA DEL CONJUNTO DE LA PROPUESTA DE ORDENACIÓN URBANA DEL ÁREA CON IMÁGENES DE RECORRIDO



1 - Frente comercial sobre el parque lineal 2 - Calle local arbolada (vista hacia el parque)

INDICADORES DE SOSTENIBILIDAD - ENFOQUE SOCIO-AMBIENTAL

MODELO DE GESTION PROPUESTO

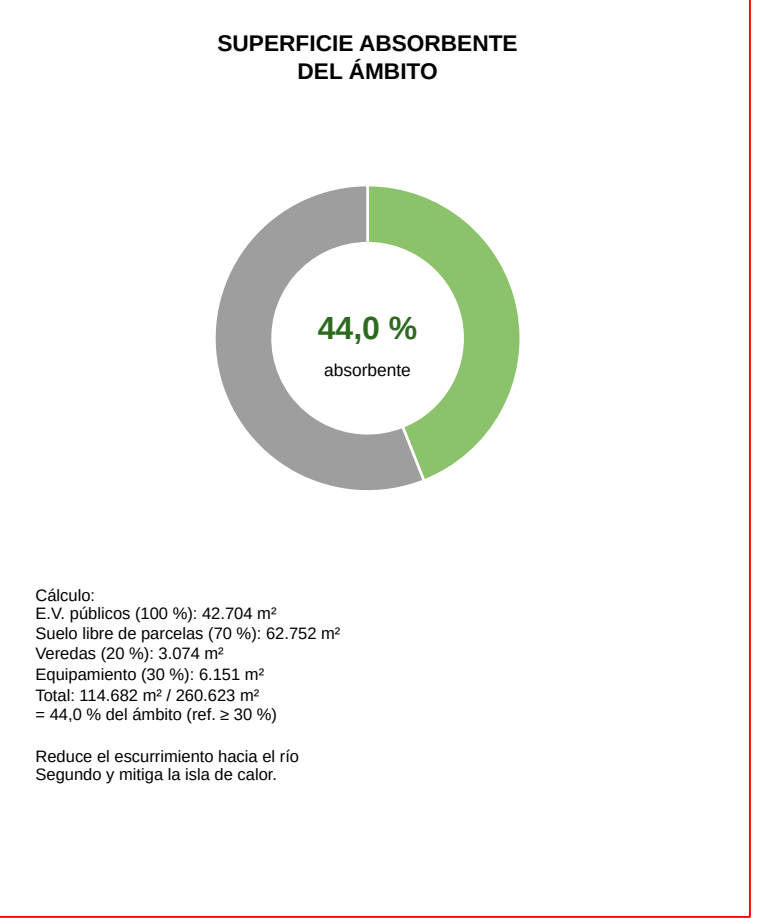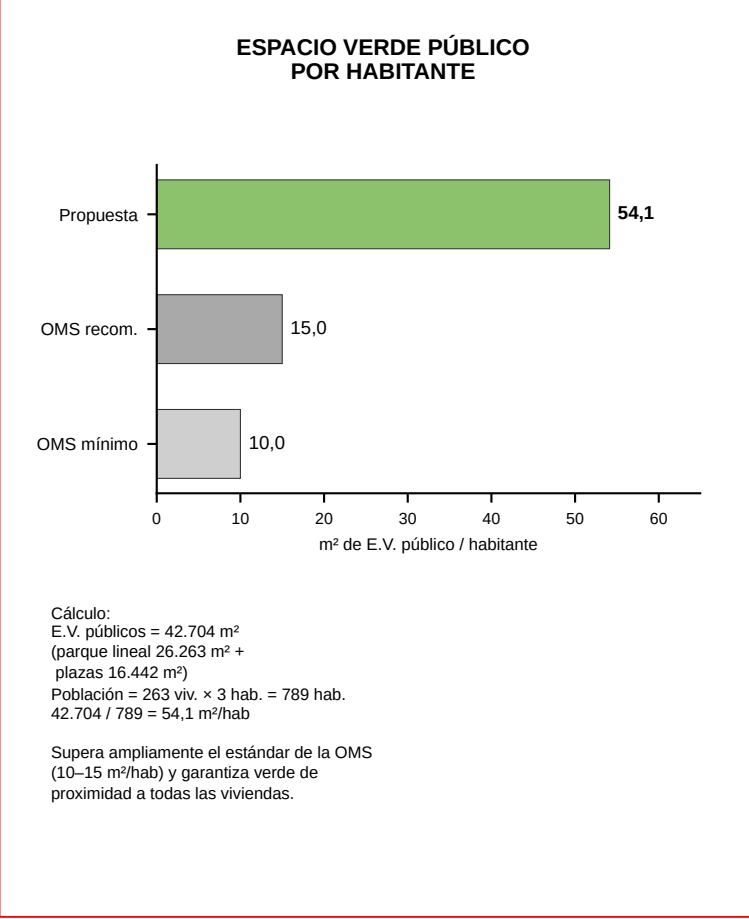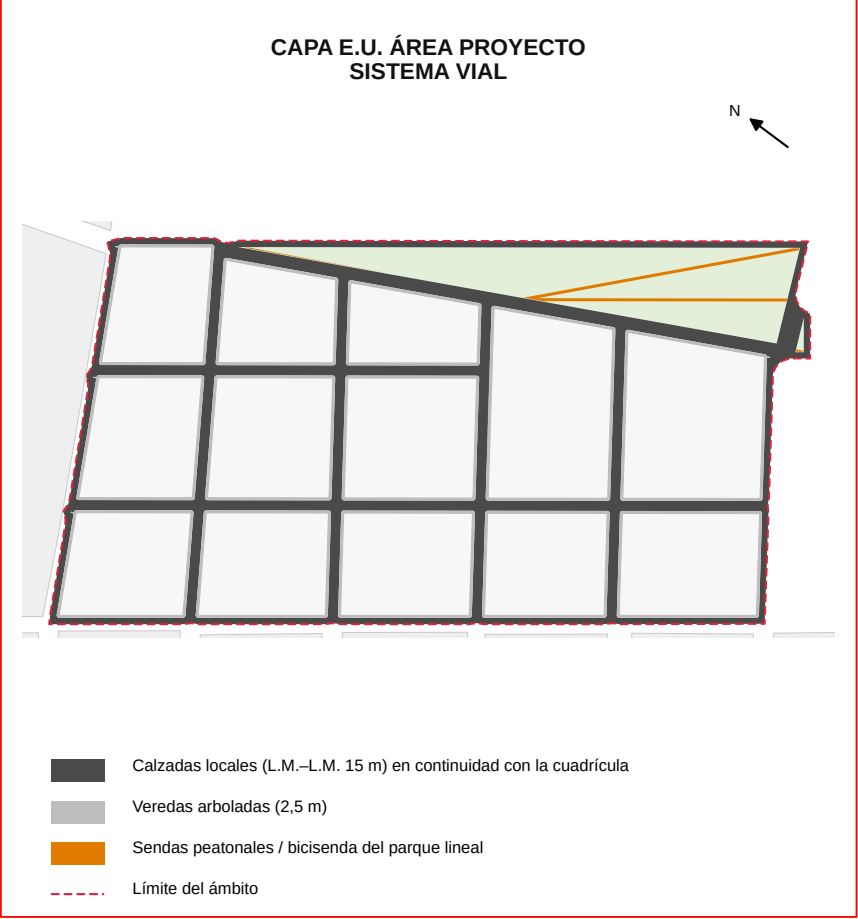

MODELO DE GESTIÓN
Contexto: urbanístico (ámbito privado (Municipalidad de Pilar y propietarios del suelo) mediante una unidad de actuación única con equipamiento de barrio).

- Cesiones gratuitas al municipio: viario, espacios verdes y equipamiento (≈47 % del ámbito).
- Recuperación de plusvalías por el caso de suelo rural a urbano, en suelo o en obras de infraestructura (agua, cloaca, pavimento, alumbrado).
- Ejecución por etapas: E1 manzanas contiguas al tejido existente (zonas de red); E2 parque lineal y frente comercial; E3 equipamiento público.
- Caso de vivienda social en la tipología R1 a través de programas provinciales y nacionales.
- Mantenimiento del parque lineal por un consorcio vecinal junto con el municipio.

789	POBLACIÓN (hab.)	263	VIVIENDAS (viv.)	30,3	DENSIDAD POBLACIONAL (hab./ha.)	10,1	DENSIDAD BRUTA (viv./ha.bruta)	19,1	DENSIDAD NETA (viv./ha.neta)	26,06	SUP. AMBITO (ha.)	5,97 22,9%	SUP. VIARIO (ha.-%)	4,27 16,4%	SUP. ESP. VERDES (ha. - %)	2,05 7,9%	SUP. EQUIP. PUB. (ha. - %)	13,77 52,8%	SUP. PARCELAS RESIDENCIALES (ha. - %)
-----	------------------	-----	------------------	------	---------------------------------	------	--------------------------------	------	------------------------------	-------	-------------------	---------------	---------------------	---------------	----------------------------	--------------	-----------------------------	----------------	--

INDICADORES URBANÍSTICOS - ENFOQUE FÍSICO-FUNCIONAL